



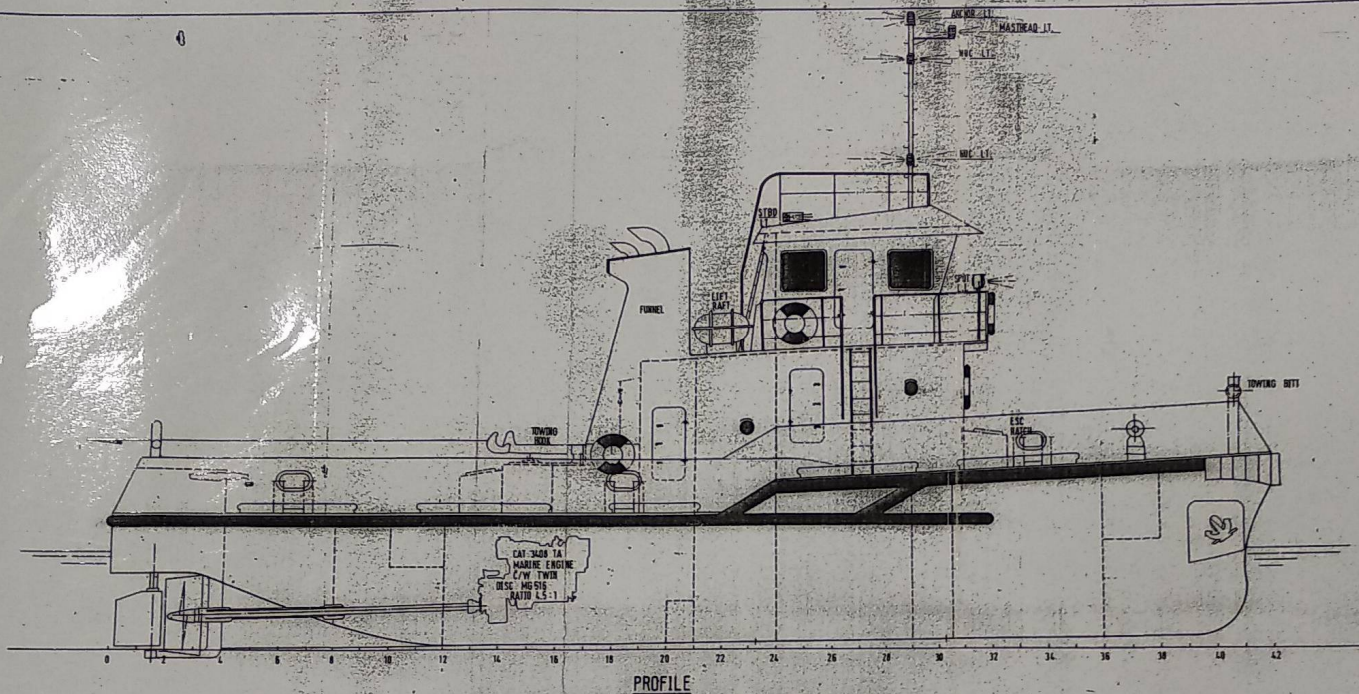


PROFILE

GENERAL PARTICULARS


L.O.A	29.00 M
L.W.L	20.88 M
L.B.P	18.54 M
Bmid	8.20 M
Dmid	2.60 M
Tload	1.85 M

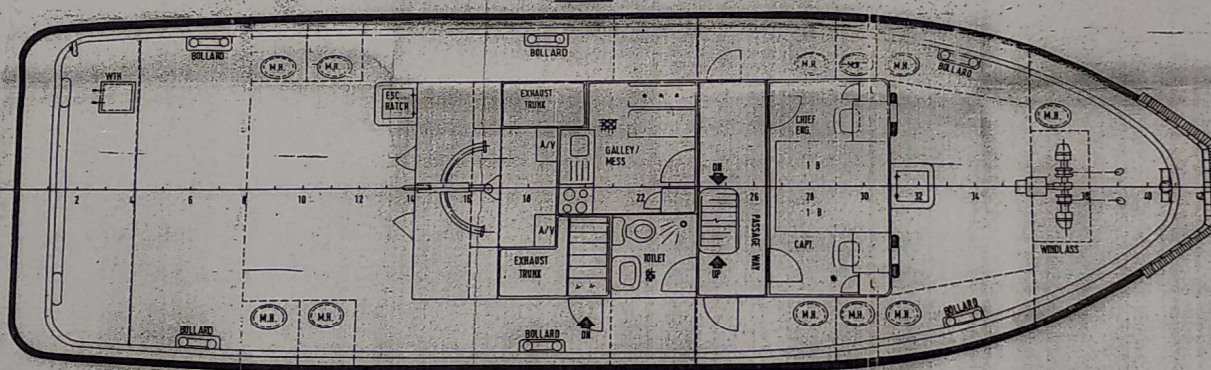

MAIN DECK PLAN

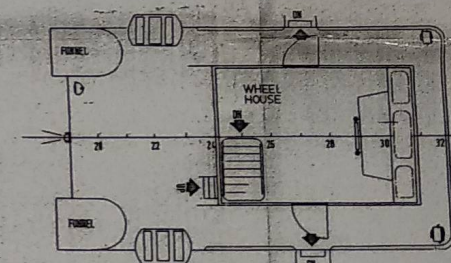

NAV. BRIDGE DECK

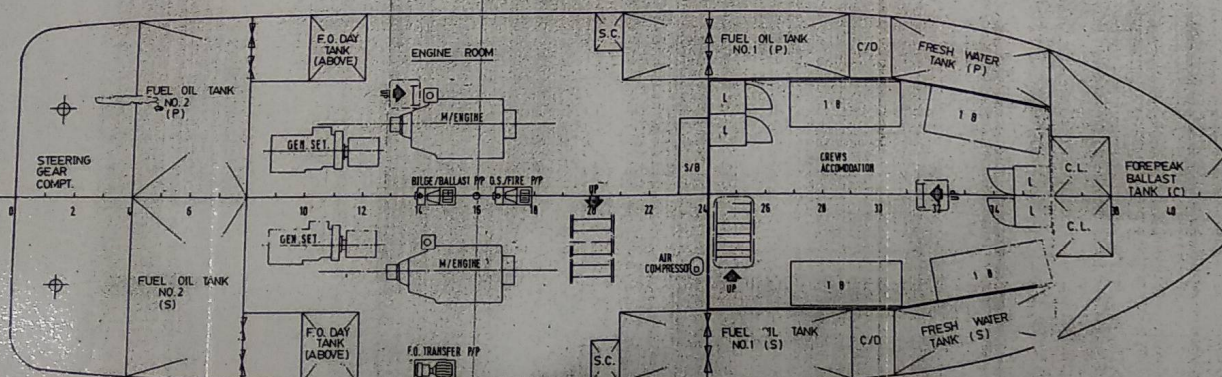

UNDER DECK PLAN

15 SEP 1991

2	AS PER DESIGN DEVELOPMENT	TING	16/10/90
1	AS PER DESIGN DEVELOPMENT	TING	10/10/90
NO.	REVISION	BY	DATE
DESIGNER  GREENBAY MARINE PTE. LTD. 4, PIONEER SECTOR 1 JURONG, SINGAPORE 2262 TEL : 8614178/9 TLX : RS 38690 BAY. TELEFAX : (65) 8618109			

21 M TWIN SCREW TUG

GENERAL ARRANGEMENT

NO.	NAME	DATE	SCALE : 1:50
APPROVED			HULL NO : P64
CHECKED			CLASS : GL
DRAWN	TING	17/02/1993	DWG. NO. : 0345/01 Rev.

THIS DOCUMENT AND THE INFORMATION IT CONTAINS IS COPYRIGHT AND REMAINS THE PROPERTY OF GREENBAY MARINE (PTE) LTD. IT IS NOT TO BE COPIED IN WHOLE OR IN PART OR DISCLOSED TO ANY THIRD PARTY FOR ANY PURPOSE WHATSOEVER WITHOUT YOUR WRITTEN CONSENT.