




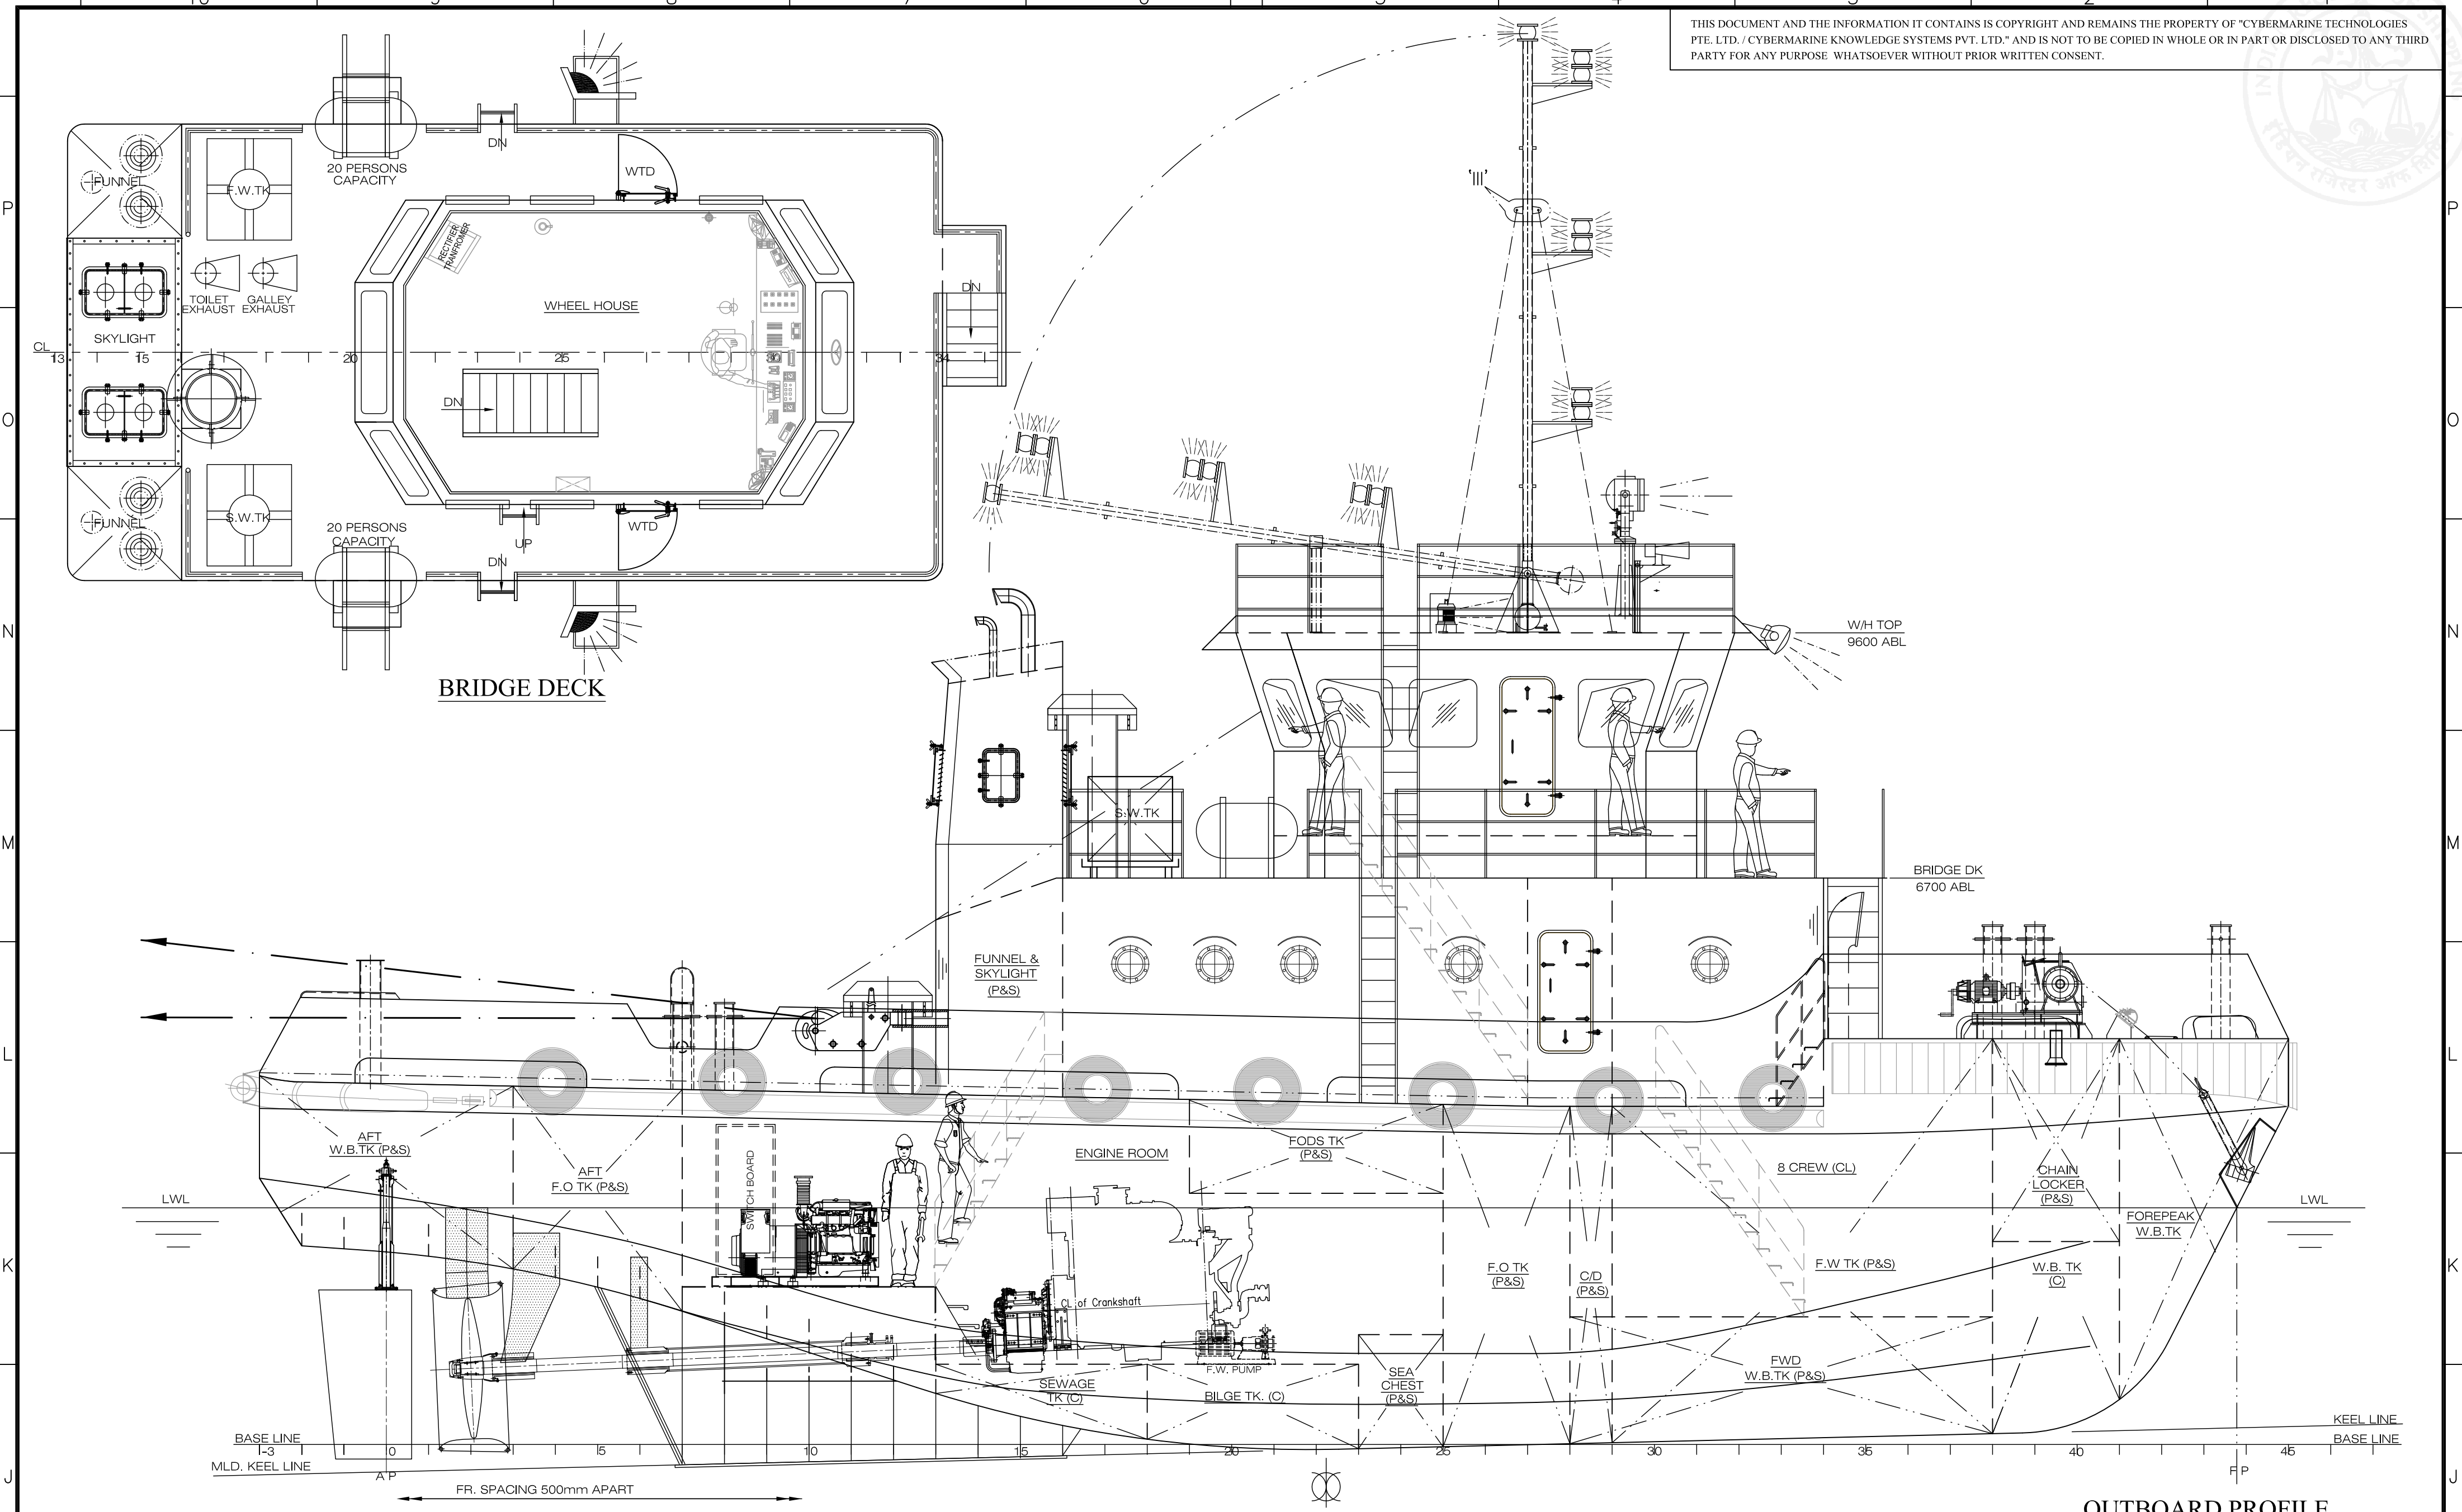

OUTBOARD PROFILE

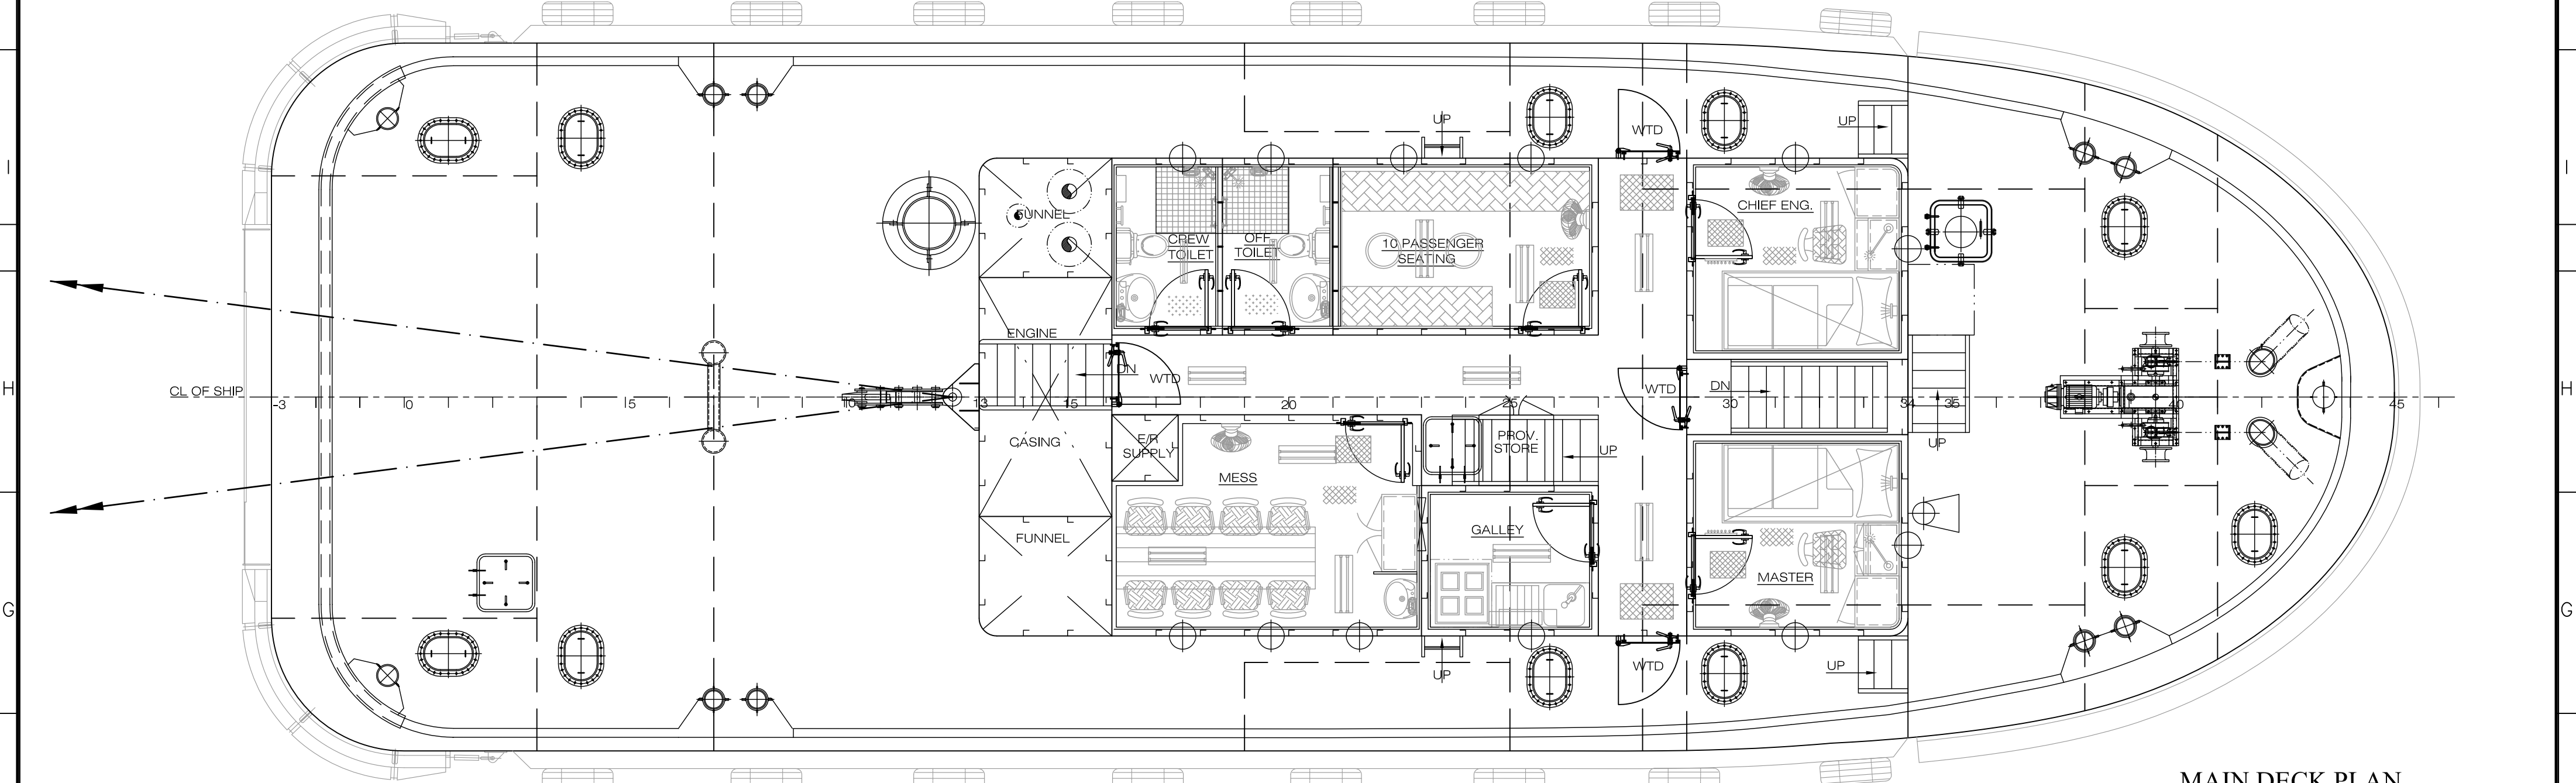

MAIN DECK PLAN

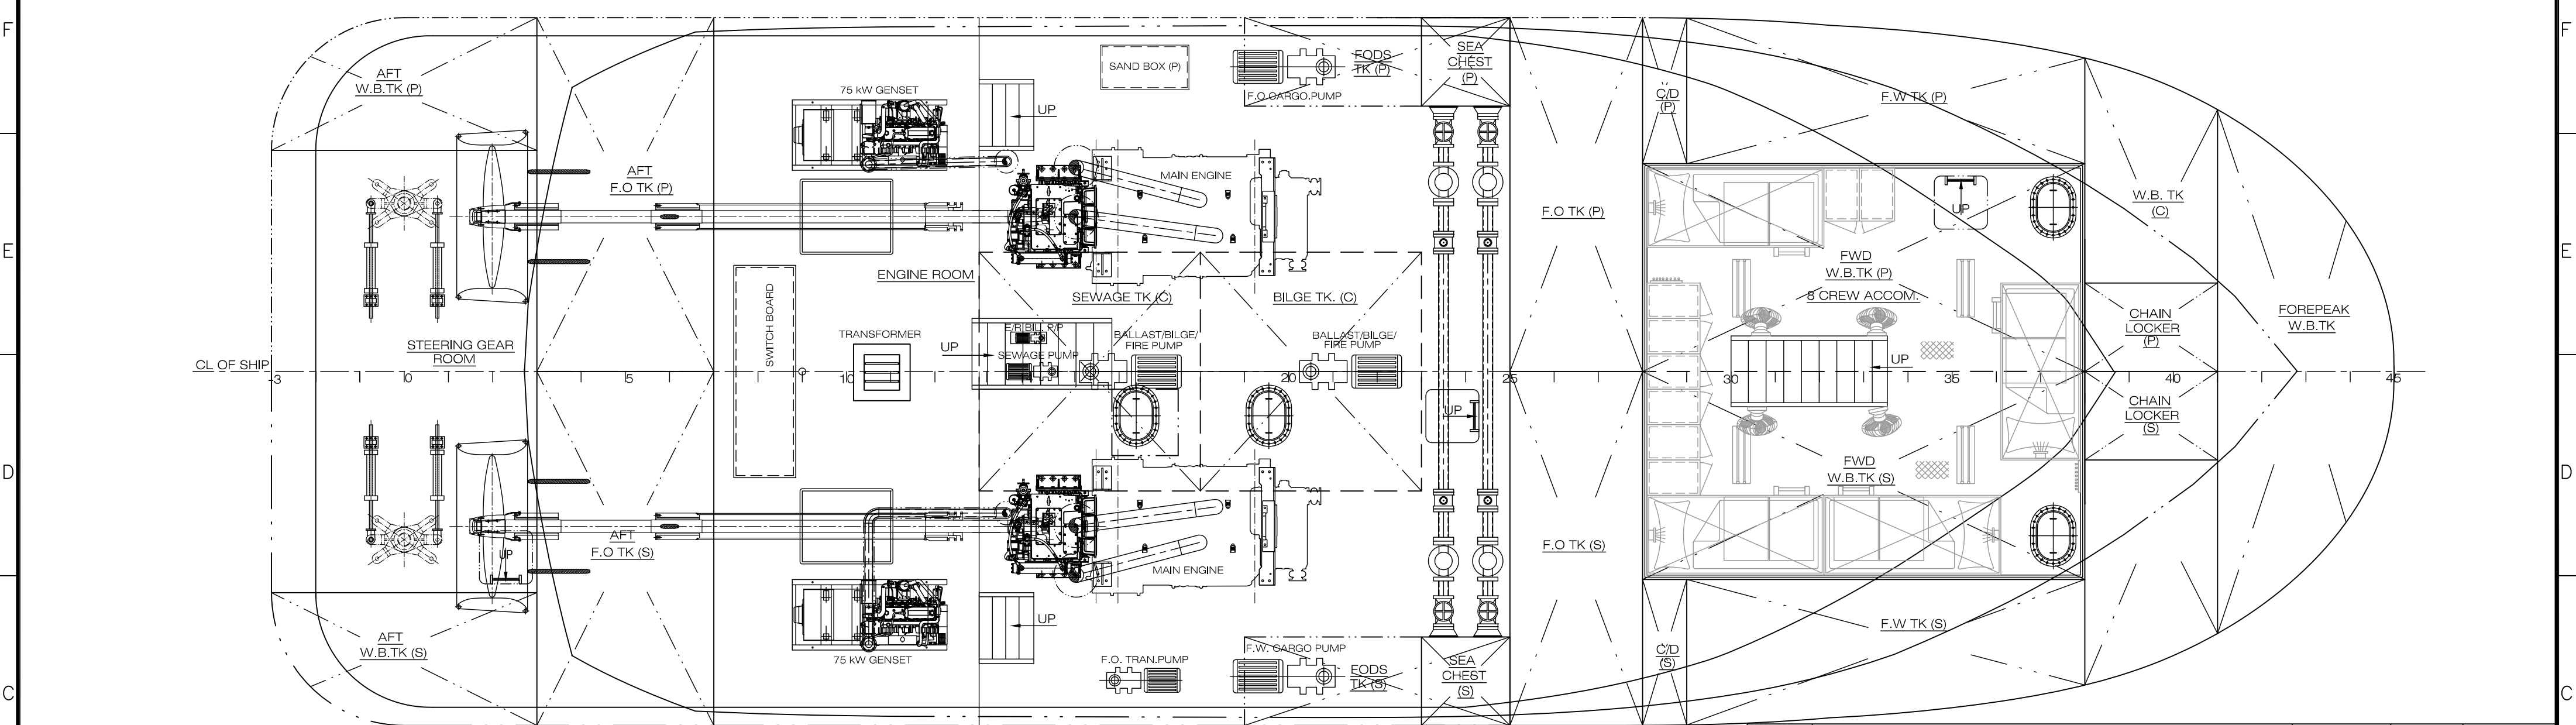

BELOW MAIN DECK PLAN

MAIN PARTICULARS

LENGTH OVERALL	24.00 M
BREADTH MLD	8.00 M
DEPTH MLD	4.00 M
DRAFT SCANTLING	3.60 M
DRAFT DESIGN	2.826 M
COMPLEMENT	10
SEATING PASSENGERS	10
MAIN ENGINES	2 x 850 BHP @ 1800 rpm
BOLLARD PULL	22 TONNE
CAPACITIES:-	
F.O.	68 TONNES
F.W.	28 TONNES

CLASS NOTATION:-

SWASTIKA * SUL, Tug, TUG
SWASTIKA * IY

DESCRIPTIVE NOTE: "INDIAN RIVER SEA VESSEL - TYPE 4"

AS AMENDED

PLAN(S) NOW SENT SUPERSEDE THE APPROPRIATE PLAN(S) PREVIOUSLY APPROVED/NOTED ON 12 JUL, 2016.

SEE LETTER : E-21000-47422

INDIAN REGISTER OF SHIPPING MUMBAI

DATE: 20 Jul 2016

NOTED FOR INFORMATION

Rev.	Description	Date	Drawn	Review
10	COMPLEMENTS ARE UPDATED.	13.07.16	GANESH	JAYASHRI
09	DRAWING REVISED AS PER YARD COMMENTS.	30.06.16	ARCHANA	JAYASHRI
08	DRAWING REVISED AS PER UPDATED SEATING ARRANGEMENT FOR PASSENGERS.	07.04.16	PRADIP	JAYASHRI
07	DRAWING REVISED AS PER TOWING ARRANGEMENT PLAN_Rev-02	21.10.15	MAHENDRA	ABHAY
06	DRAWING REVISED AS PER TOWING ARRANGEMENT PLAN	13.08.15	MAHENDRA	ABHAY
05	DRAWING REVISED AS PER LOAD LINE PLAN REV.02	07.05.15	MAHENDRA	ABHAY

Rev.	Description	Date	Drawn	Review
04	WHEEL HOUSE & FUNNEL MODIFIED AS PER YARD RECOMMENDATION	13.02.15	ABHAY	SHAIKESH
03	BOLLARD PULL REVISED	23.12.14	ARCHANA	JERIN
02	DRAFT SCANTLING REVISED	18.12.14	PRASAD N.	ABHAY
01	UPDATE CLIENT NAME AND YARD NO.	16.12.14	PRASAD N.	ABHAY
Issued for		Construction		
Builder		Project		
GMS MARINE SERVICES, JAMNAGAR		RISHI VISTARA-1 (YARD NO. GMS / 01)		
Drawing Title		GENERAL ARRANGEMENT		
Scale		1:50		
Size		A1		
Date		01/12/2014		
Sheet		1 of 1		
Drawn		MEENA		
Checked		KAAMRAN		
Review-1		SAUMYA		
Review-2		SHAIKESH		

Cybermarine Knowledge Systems Pvt. Ltd.
"TECHNOCTIVITY" Unit No. 501-505 Plot No. X-5/3,
TTC Industrial Area, Opp. Millennium Business Park,
Mahape - MIDC, Navi Mumbai 400710.
Tel : +91 22 61462400 (10 Lines) , Fax. +91 22 61462411.
E-mail : info@cybermarine.net, website : www.cybermarine.net