




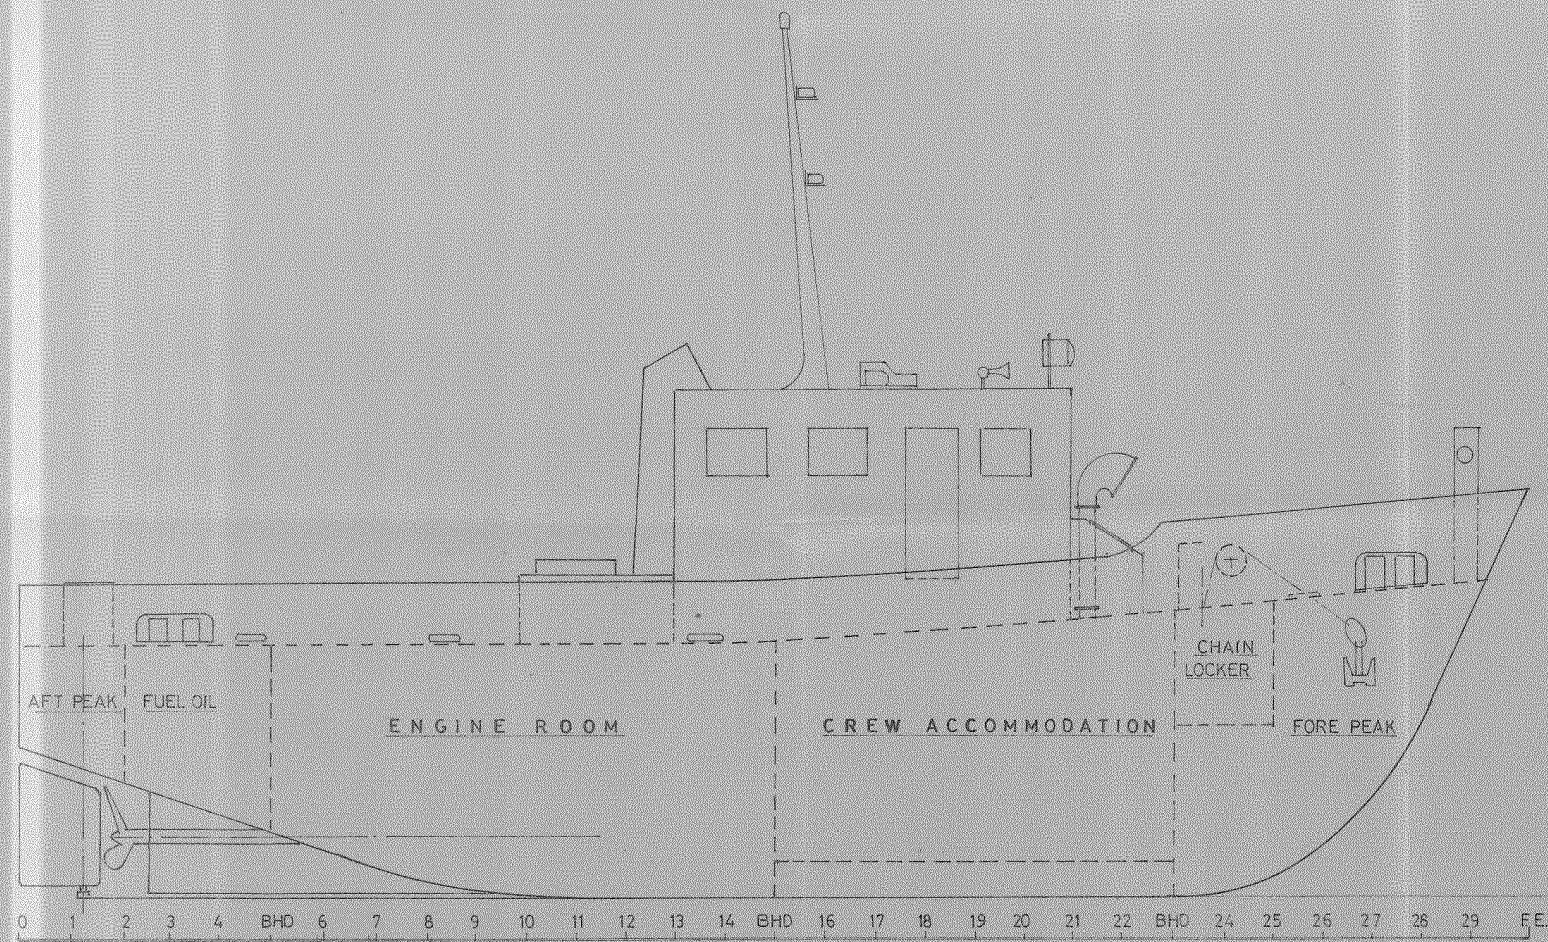

PROFILE

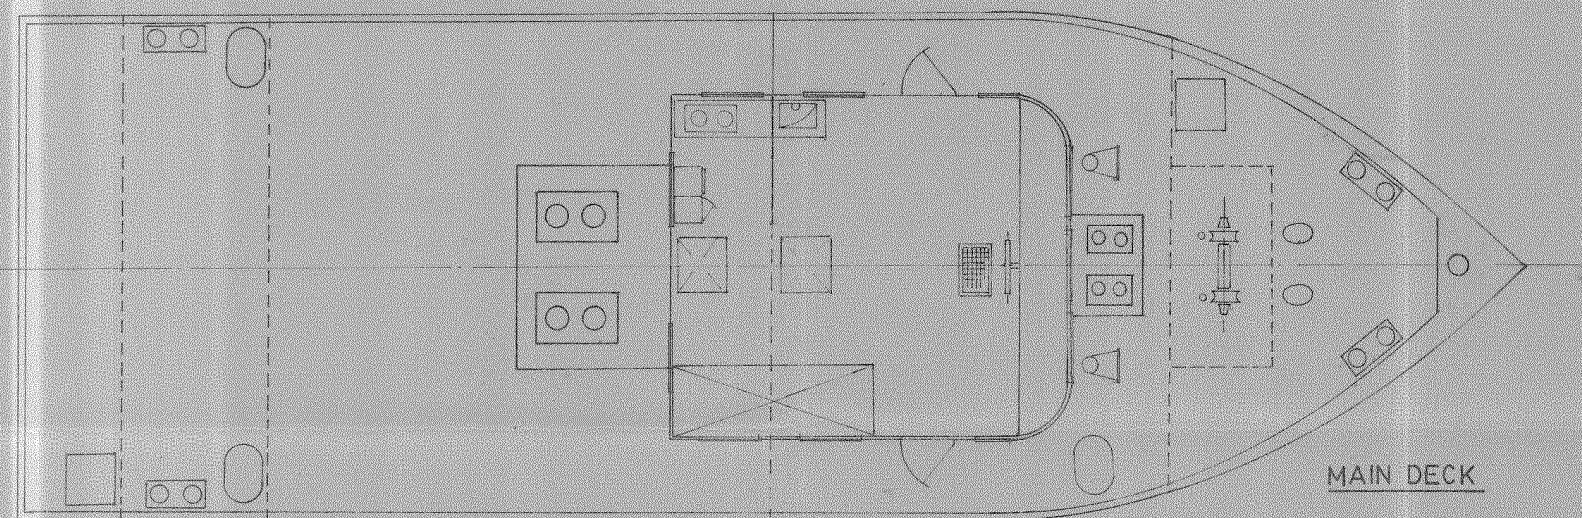

MAIN DECK

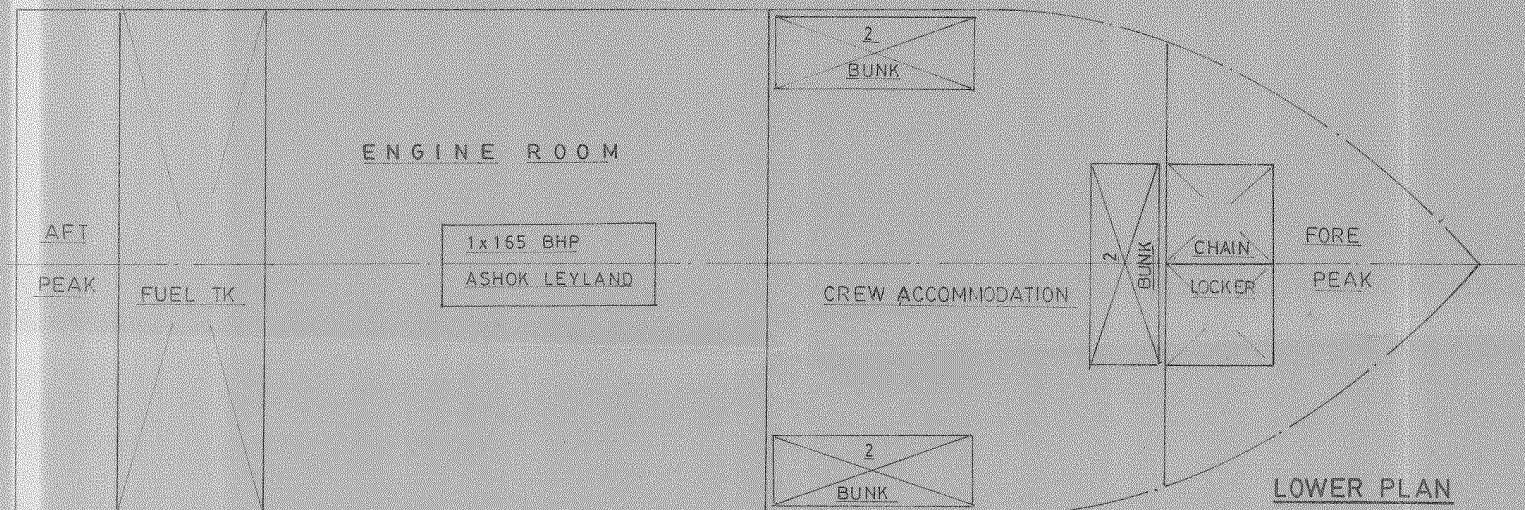

LOWER PLAN

MAIN PARTICULARS

LENGTH	: 15.0 M
BREADTH	: 5.0 M
DEPTH	: 2.5 M
DRAFT	: 1.7 M
SERVICE	: INLAND WATERS.
ENGINE	: ASHOK LEYLAND 1x165 BHP AT 1800 RPM.

CLIENT	M/s HINDUSTAN SEA - LINK AGENCIES.	YARD NO.	CLASS APPVD. ON
			MMD APPVD. ON
TITLE	GENERAL ARRANGEMENT	SCALE	DRAWN Anwar Solkar
			CHECKED
PROJECT NO.	2035 - 9013	DRAWING NO.	2035 - 9013 - 01

NATH & ASSOCIATES

C-4 Trilok, Ambedkar Road, Bandra (W).