

PRINCIPAL PARTICULARS:-


LENGTH O.A	:	50.00 M
BREADTH MLD.	:	15.00 M
DEPTH MLD.	:	3.00 M
DESIGN DRAFT	:	2.20 M
SCANTLING DRAFT	:	2.50 M
FRAME SPG.	:	500 mm

CLASS NOTATION:-


55 SU PONTON, DECK STRENGTHENED FOR 10 ton², FOR CRANE OPERATION

CRANE SPECIFICATION:-


CRANE WEIGHT = 250 T
LIFTING CAPACITY = 36.60 T
OPERATING RADUIS = 18 M
MAKE/MODEL : LIEBHERR LR 1250
BOOM/JIB : 74m MAIN BOOM, NO JIB
CRAWLERS : TWO 7520x1200 TRACKS, SEPARATED BY 7.0m

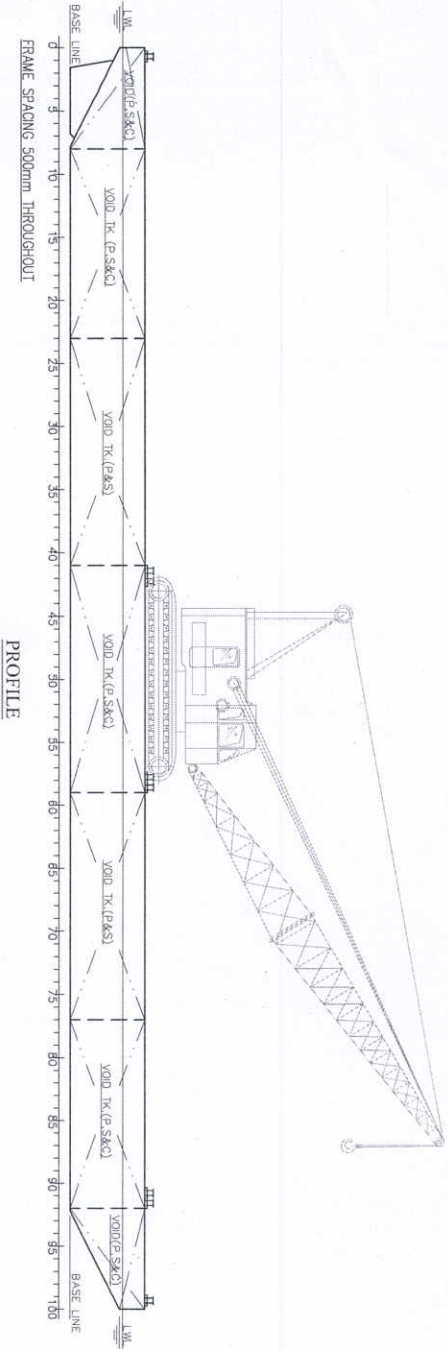

PROFILE

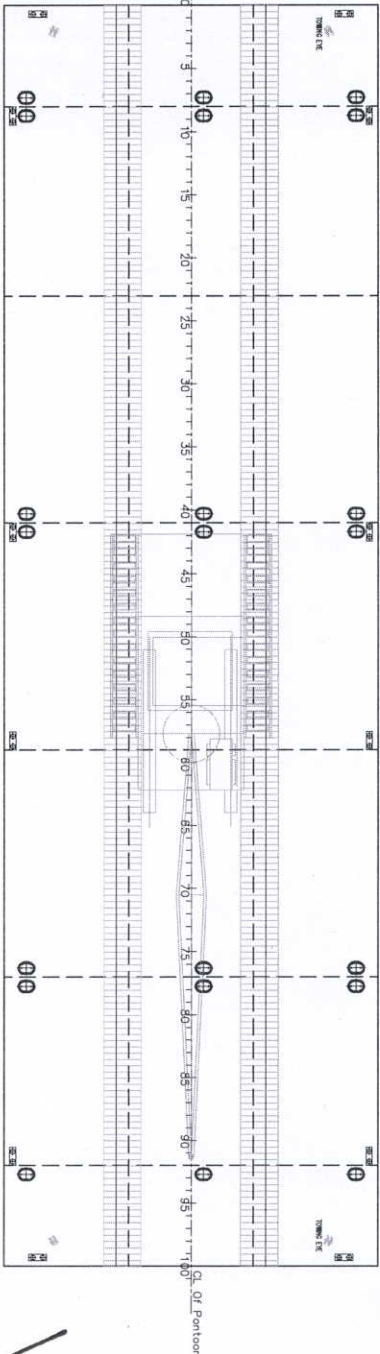

MAIN DECK PLAN

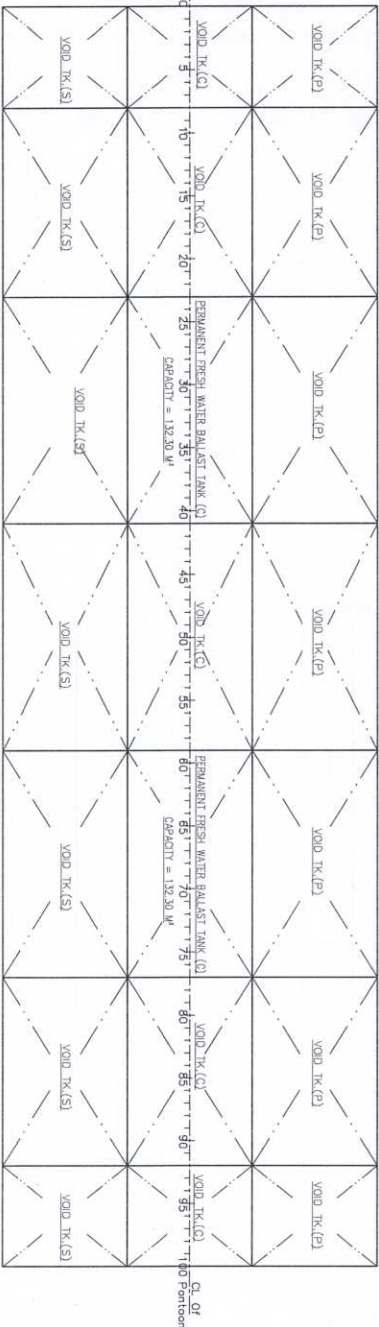

BELOW DECK PLAN

NOTE : ALL THE TANKS ARE DECLARED AS VOID TANKS HOWEVER THE STRUCTURE FOR THE SAME IS CHECKED FOR FULLY LOADED WITH LIQUIDS FOR STABILITY REQUIREMENT THE TWO TANKS DECLARED AS PERMANENT FRESH WATER BALLAST.



ARVIND PORT AND INFRA LIMITED
Director

Rev.#	Description	Date	Drawn	Review
1	Issued for			
2				
3				
4				
5				
6				
7				
8				
9				
10				
11				
12				

Client	KB SHIPPING & CO. (JAMNAGAR)	Project	PONTON
Builder	CHISTI MARINE ENGINEERING WORKS		(YARD NO. CHISTI / 023)
Dwg.#	CM22-VI-112-0001	Rev.#	Drawing Title
Scale	Scale 1:20	Date	11/09/2022
Sheet	1 of 1	Drawn	ISWAR
Checked	CHAKAR	Reviewed	MOHIT
Reviewed	SAHAY	Reviewed	SAHAY