




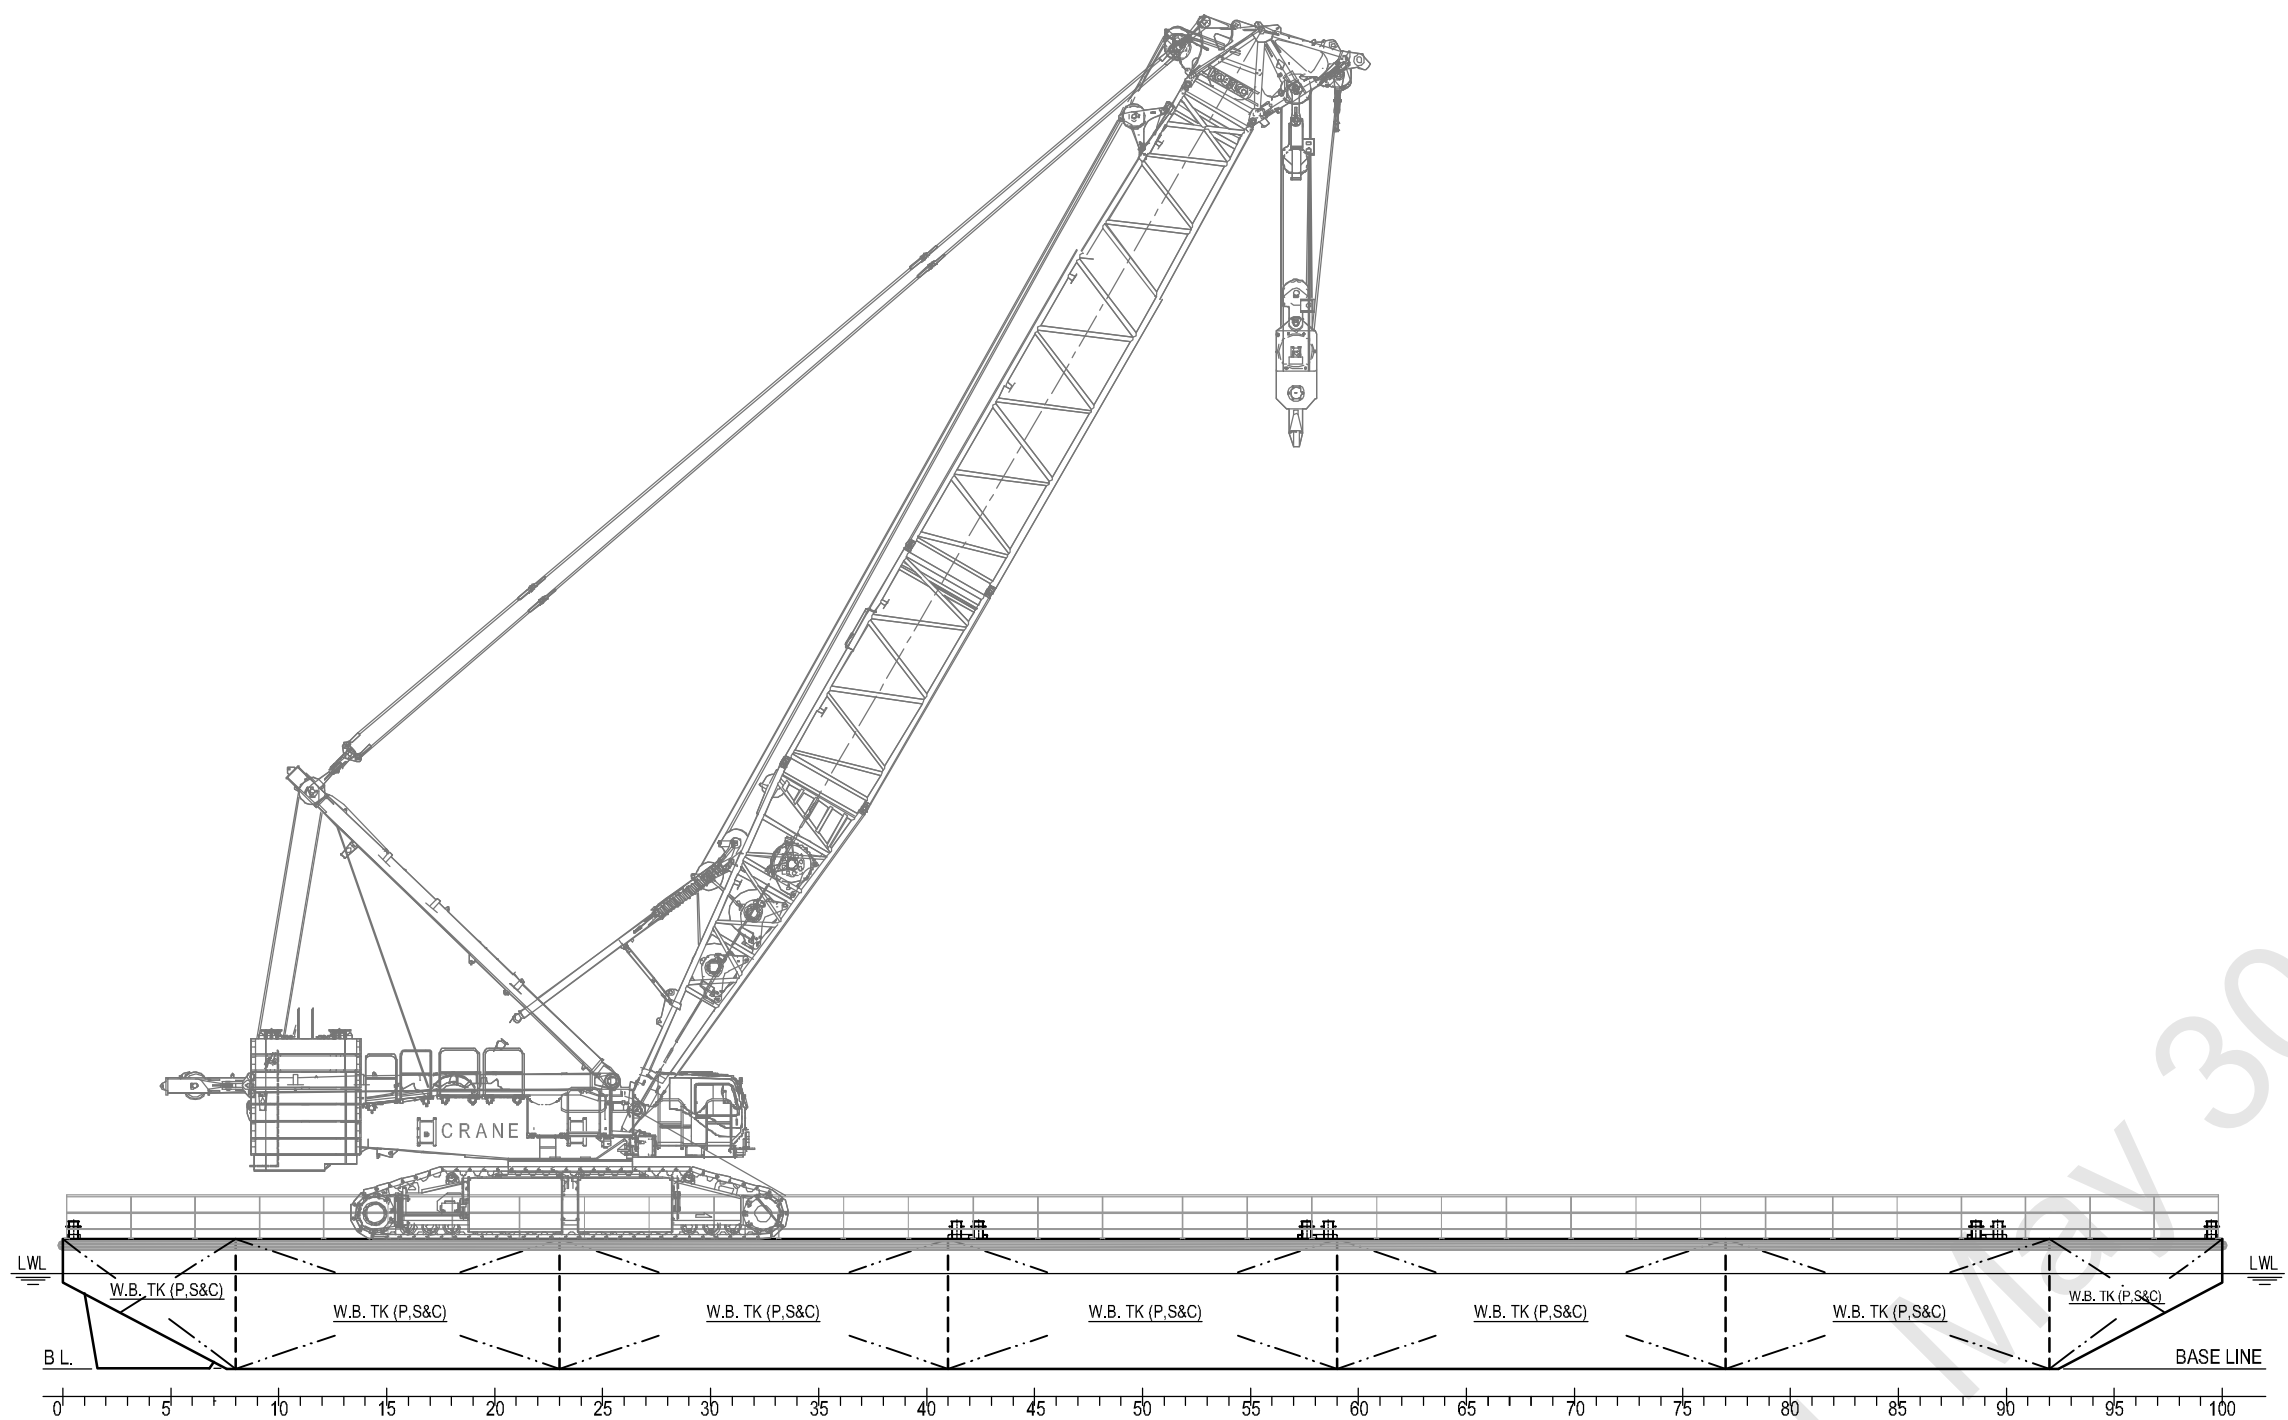

PROFILE

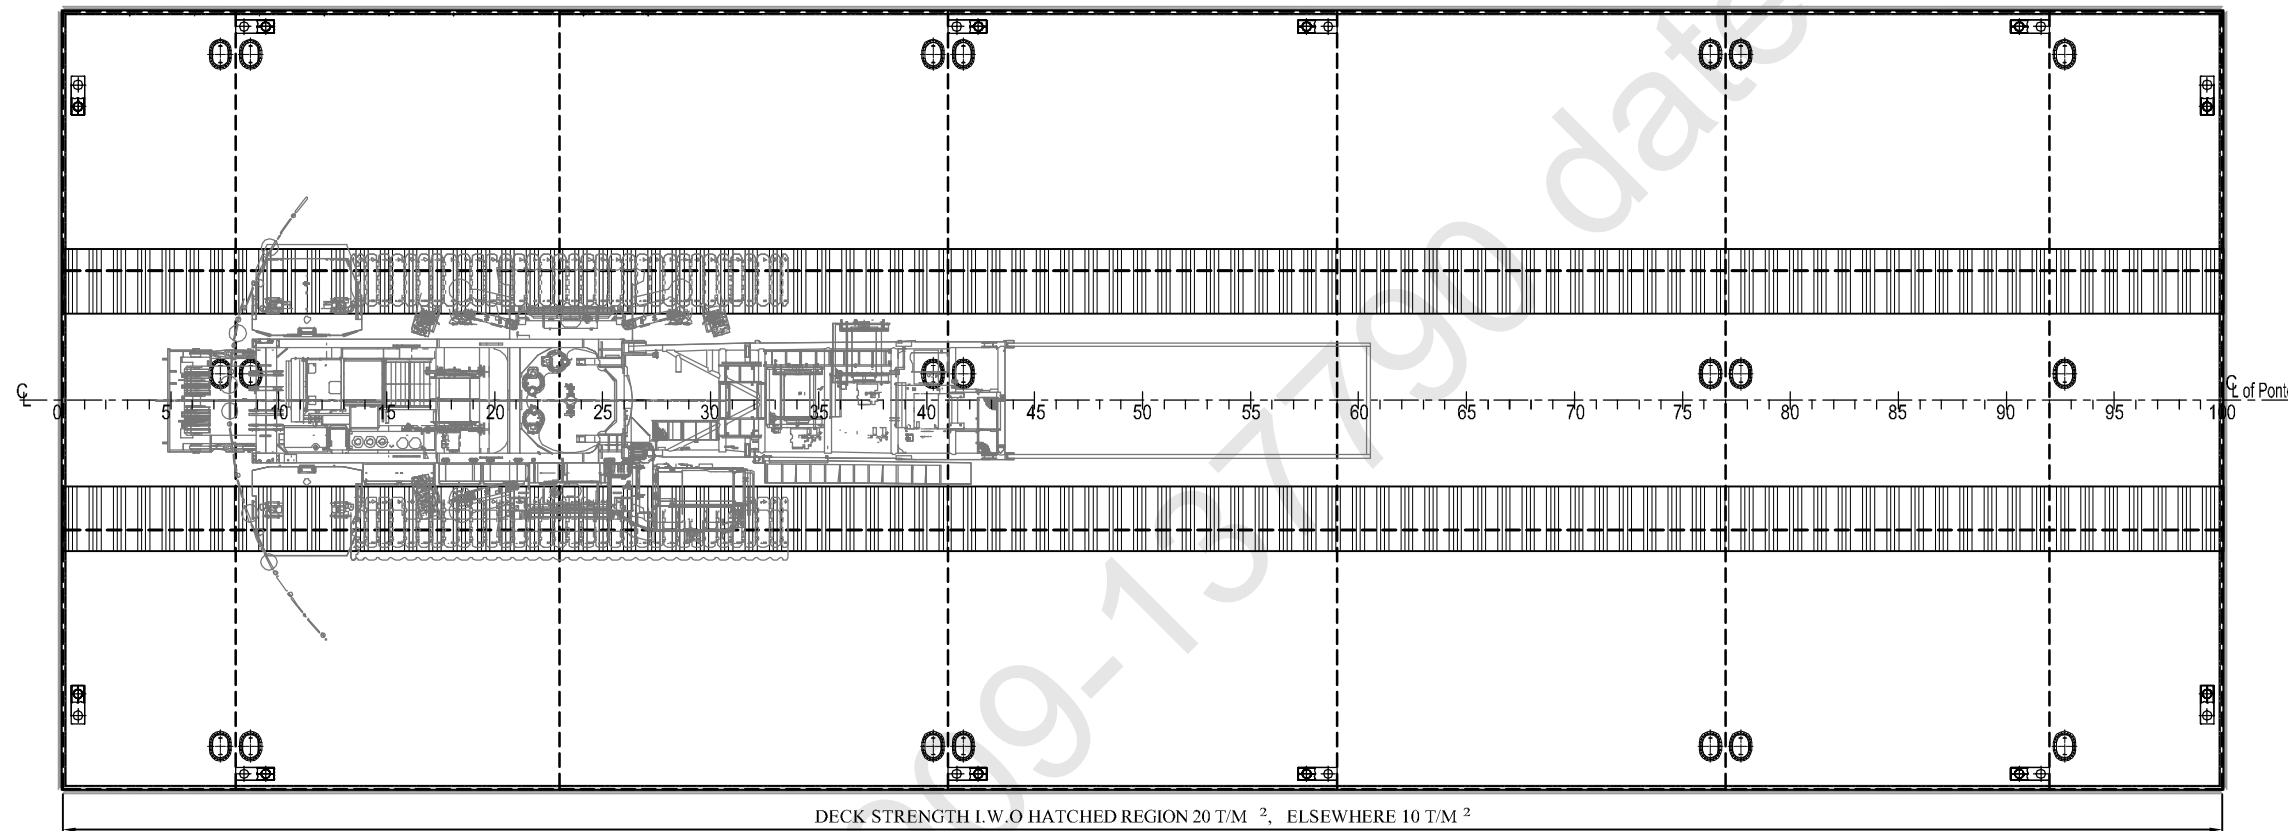

MAIN DECK PLAN

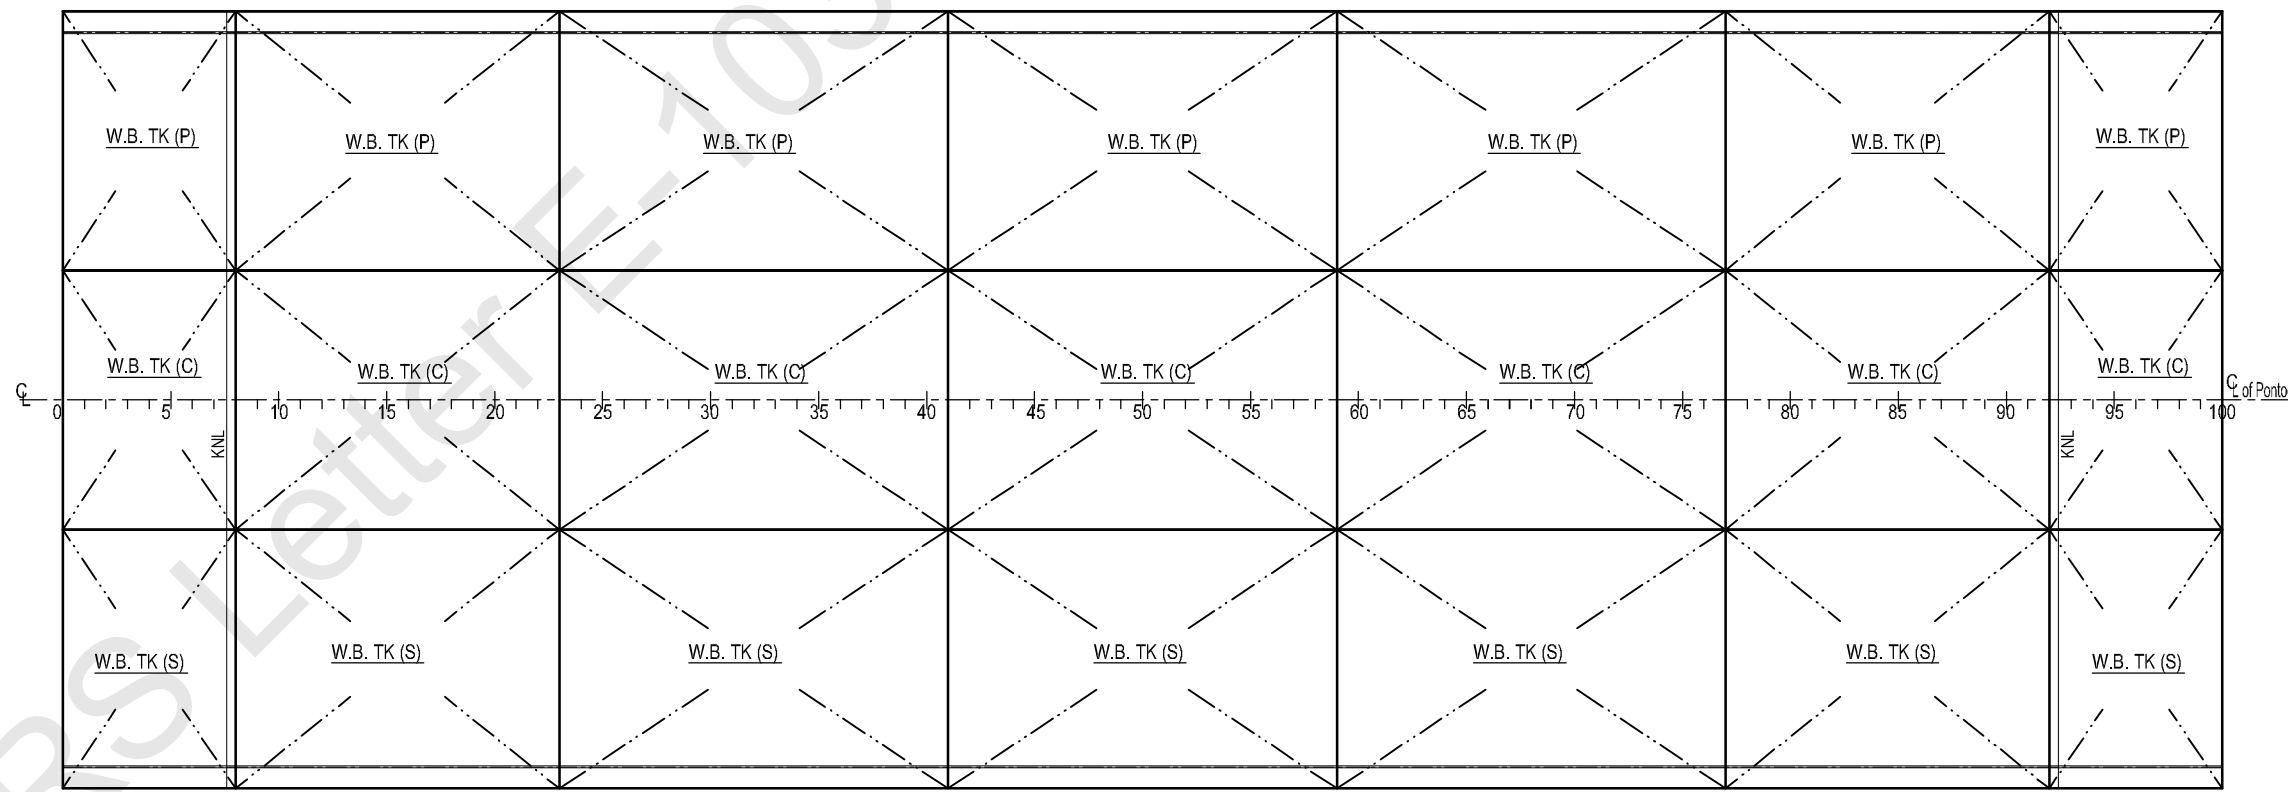

BELOW DECK PLAN

PRINCIPAL PARTICULARS:-

LENGTH O.A.	:	50.00 M
BREADTH MLD.	:	18.00 M
DEPTH MLD.	:	3.00 M
DESIGN DRAFT	:	2.20 M
SCANTLING DRAFT	:	2.60 M
FRAME SPG.	:	500 mm

CRANE SPECIFICATION:-

CRANE WEIGHT	=	350T
CRANE CAPACITY	=	40 T
WORKING RADIUS	=	29 M

SEE LETTER E-103909-137790



CLASS NOTATION:-

LS SU, PONTOON, "INDIAN COASTAL SERVICE"
Descriptive Notation: "DECK STRENGTHENED FOR 10 T/M²",
"FOR CRANE OPERATION"

NOTE:

- 1) ALL DIMENSION ARE IN MM.
- 2) CRANE WILL OPERATE ONLY IN THE HATCHED REGION.

01	DRAWING UPDATED AS PER CLIENT COMMENTS	23.05.2020	ISHWAR	SHAILESH
Rev.#	Description	Date	Drawn	Review
Issued for		Approval		
Client		Project		
K.B. SHIPPING & CO.		PONTOON		
Builder		(YARD NO. CHISTI 013 & 014)		
CHISTI MARINE SERVICES				
Drg.#	Rev.#	Drawing Title		Drawn
CM20-V-110-0001	01	GENERAL ARRANGEMENT		ISHWAR
Scale	Size	Date	Sheet	Checked
1:175	A2	18.05.2020	1 of 1	JASIM
				Review-1
				MOHIT
				Review-2
				SUDHEESH



10, Bukit Batok Crescent,
#12-01, The Spire Building,
Singapore-658079.

501, Technocity IT Premises Co-op. Soc. Ltd,
Plot No. X-5/3, Mahape,
Maharashtra- 400710, India.

22503, Katy Freeway #7,
Katy, Texas,
USA 77450.