




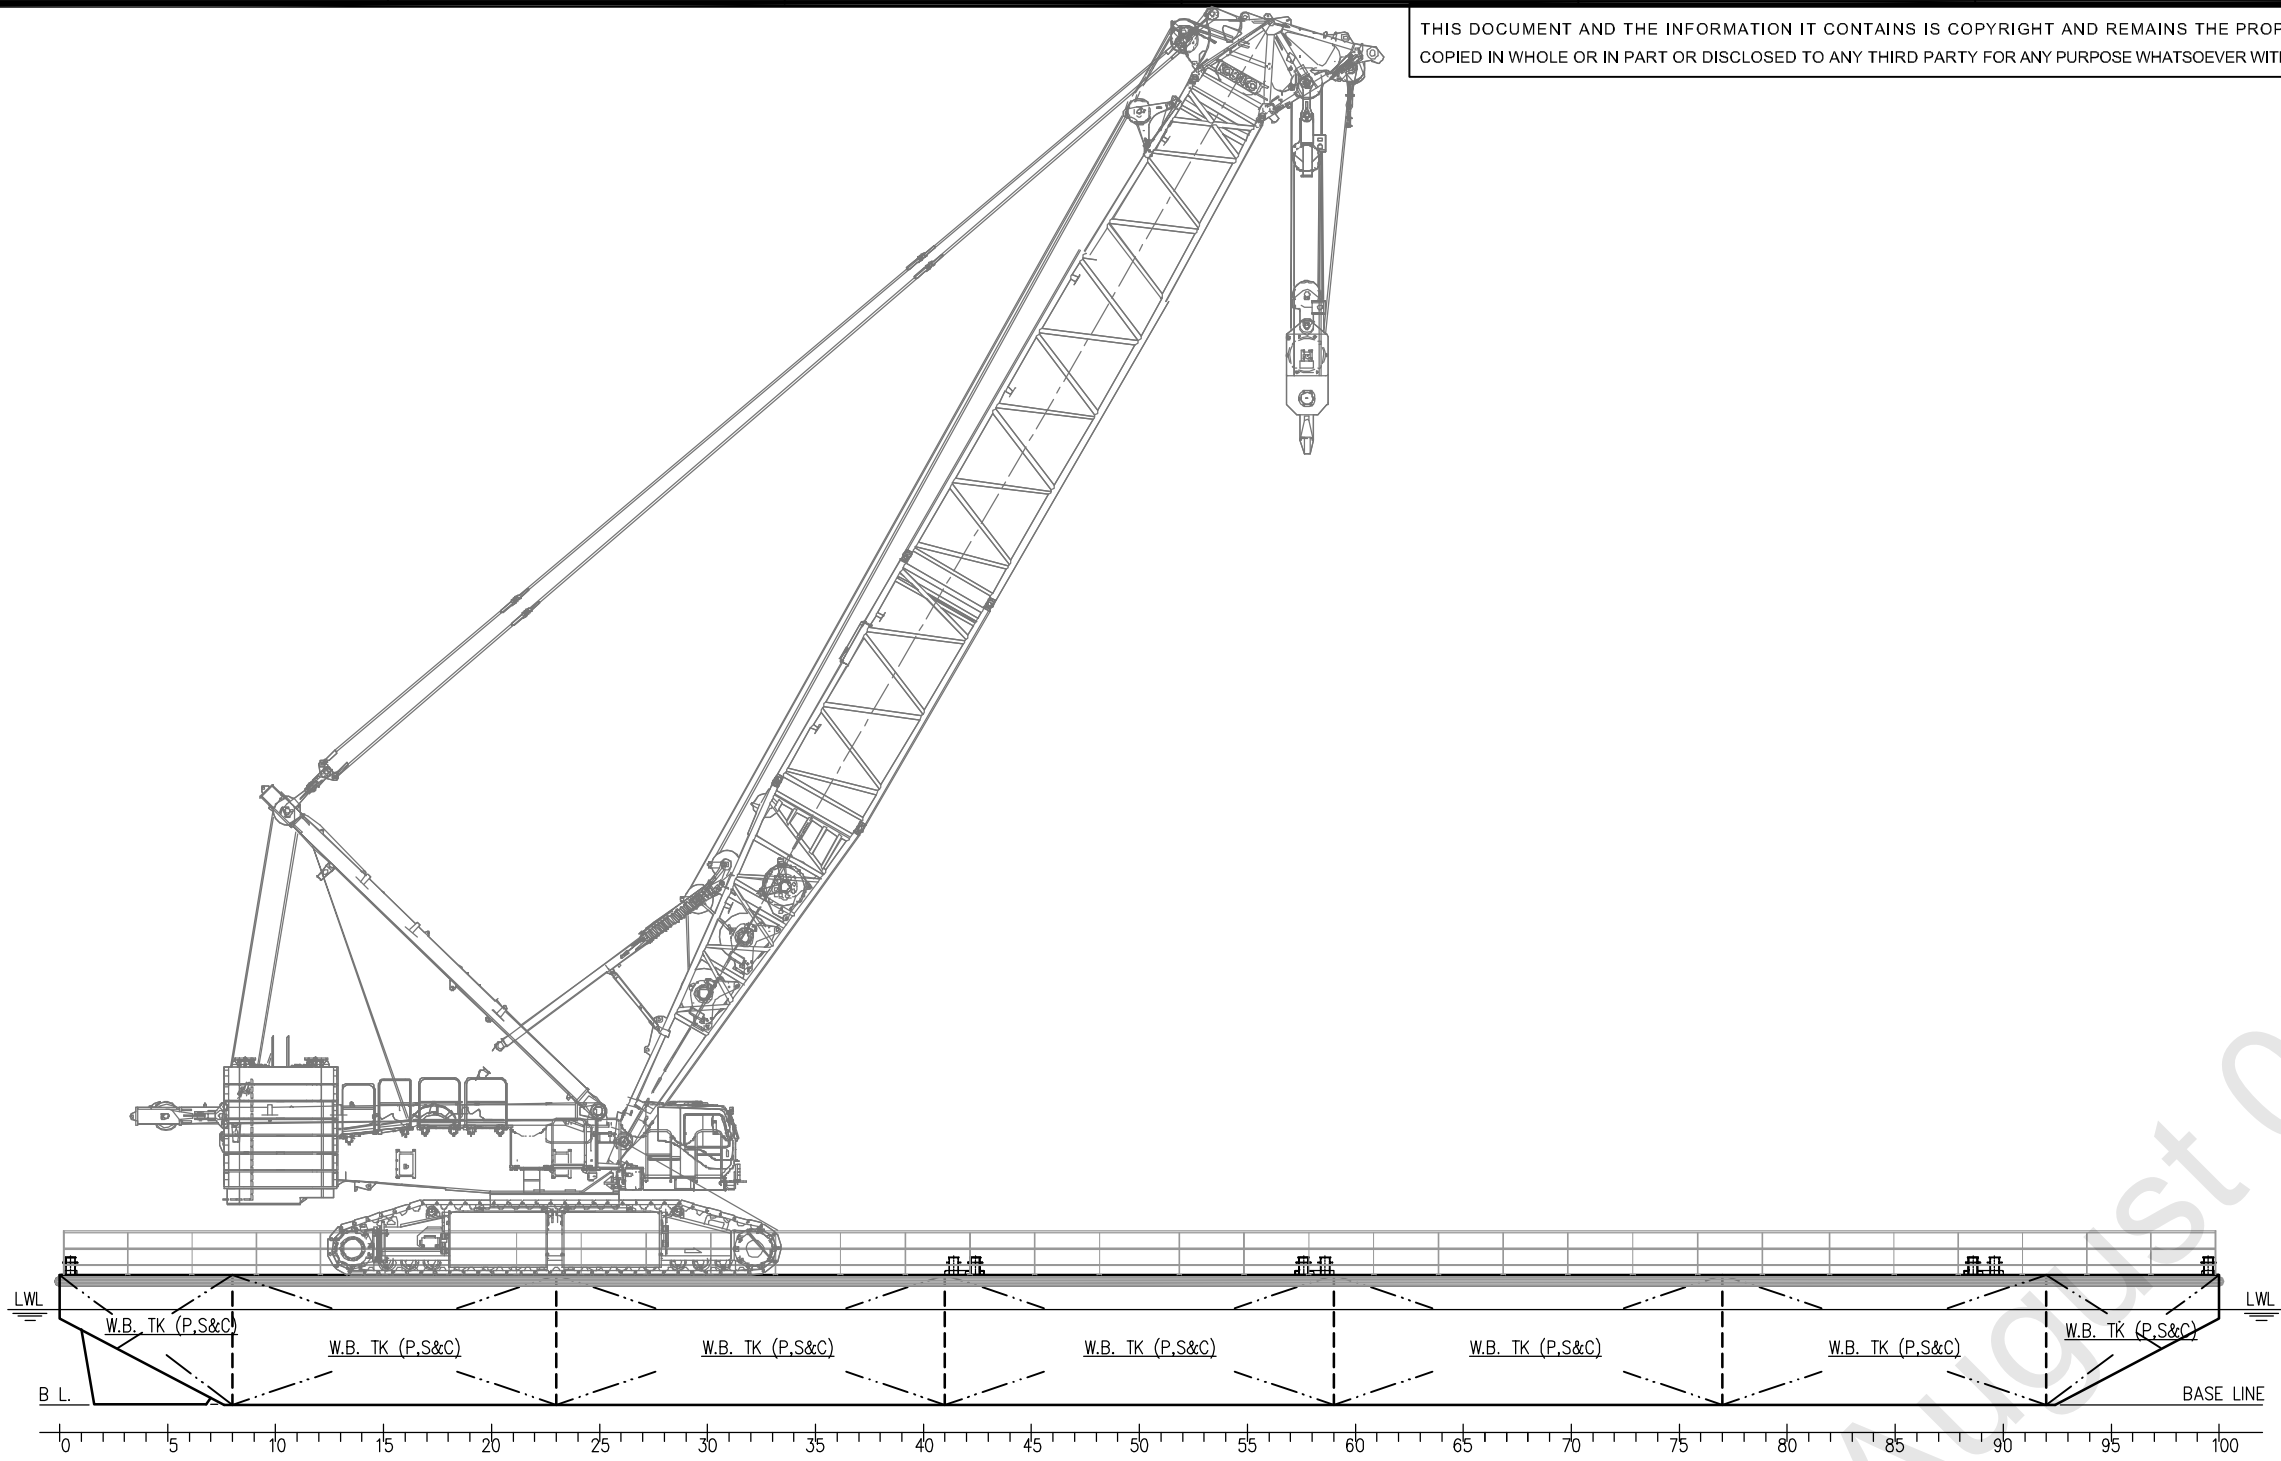

PROFILE

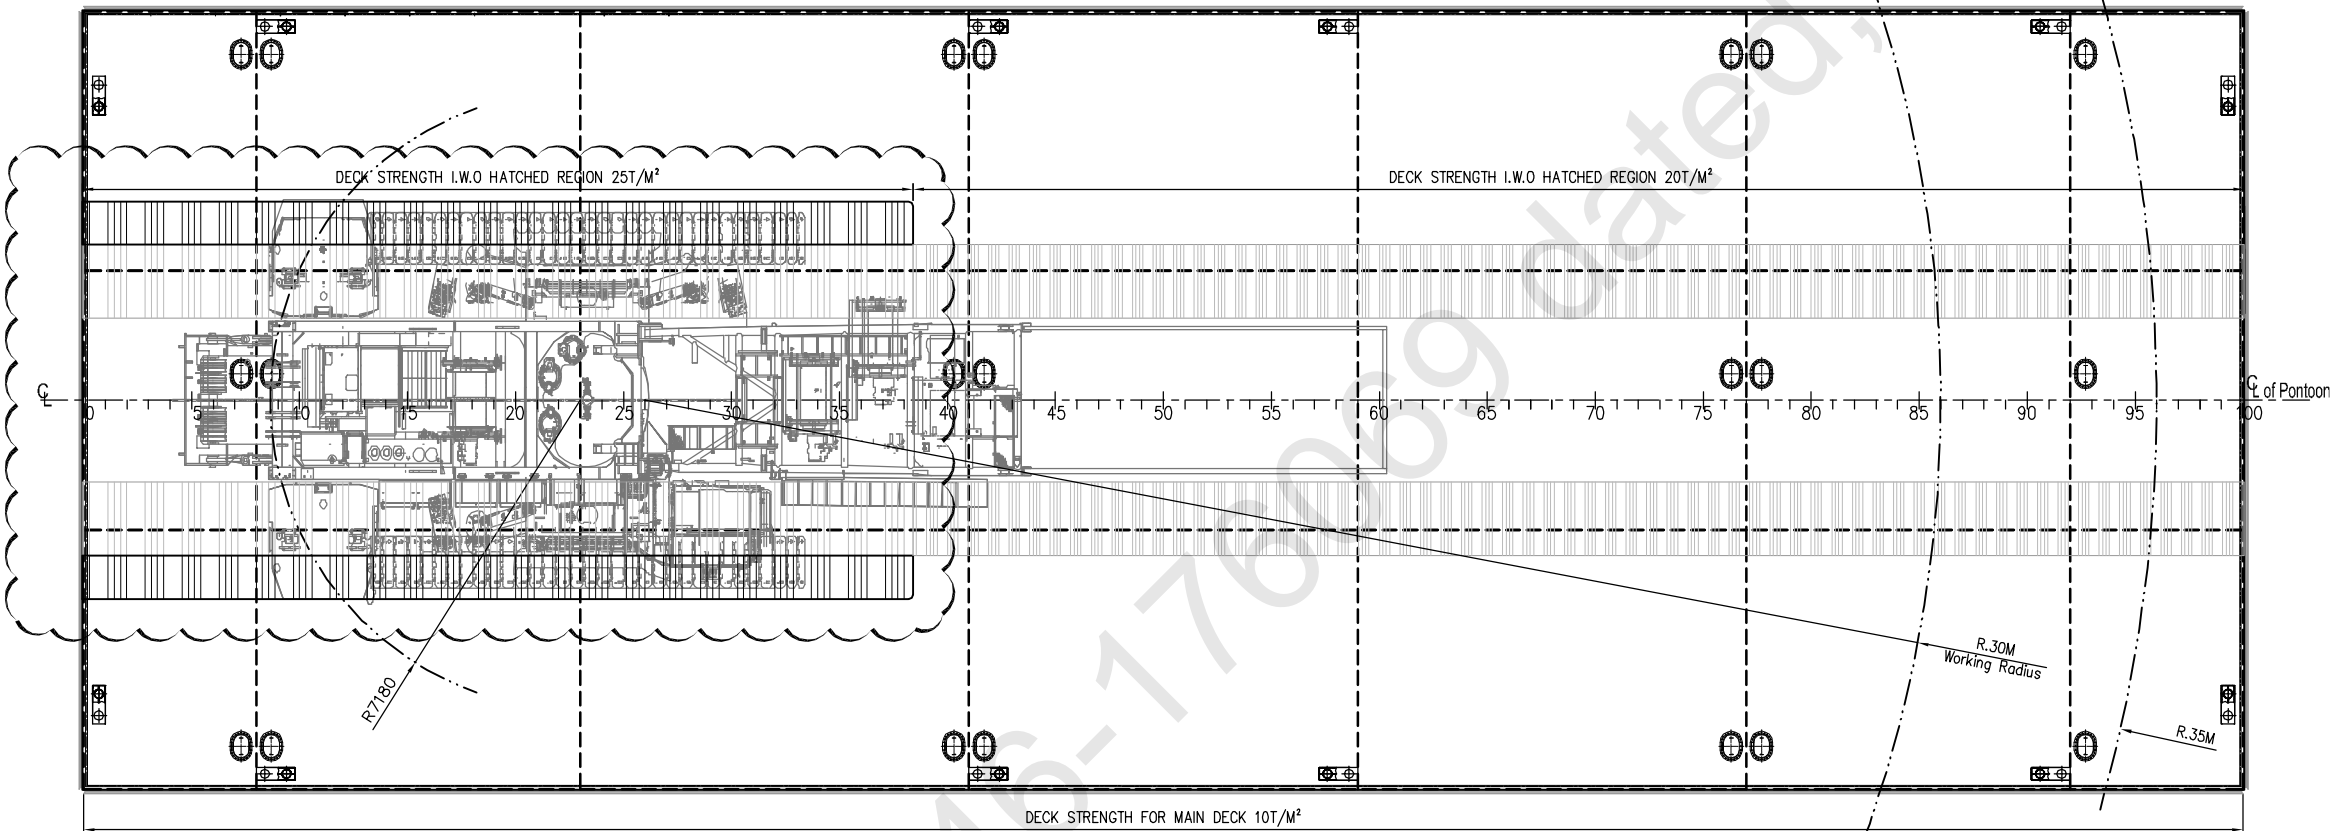

MAIN DECK PLAN

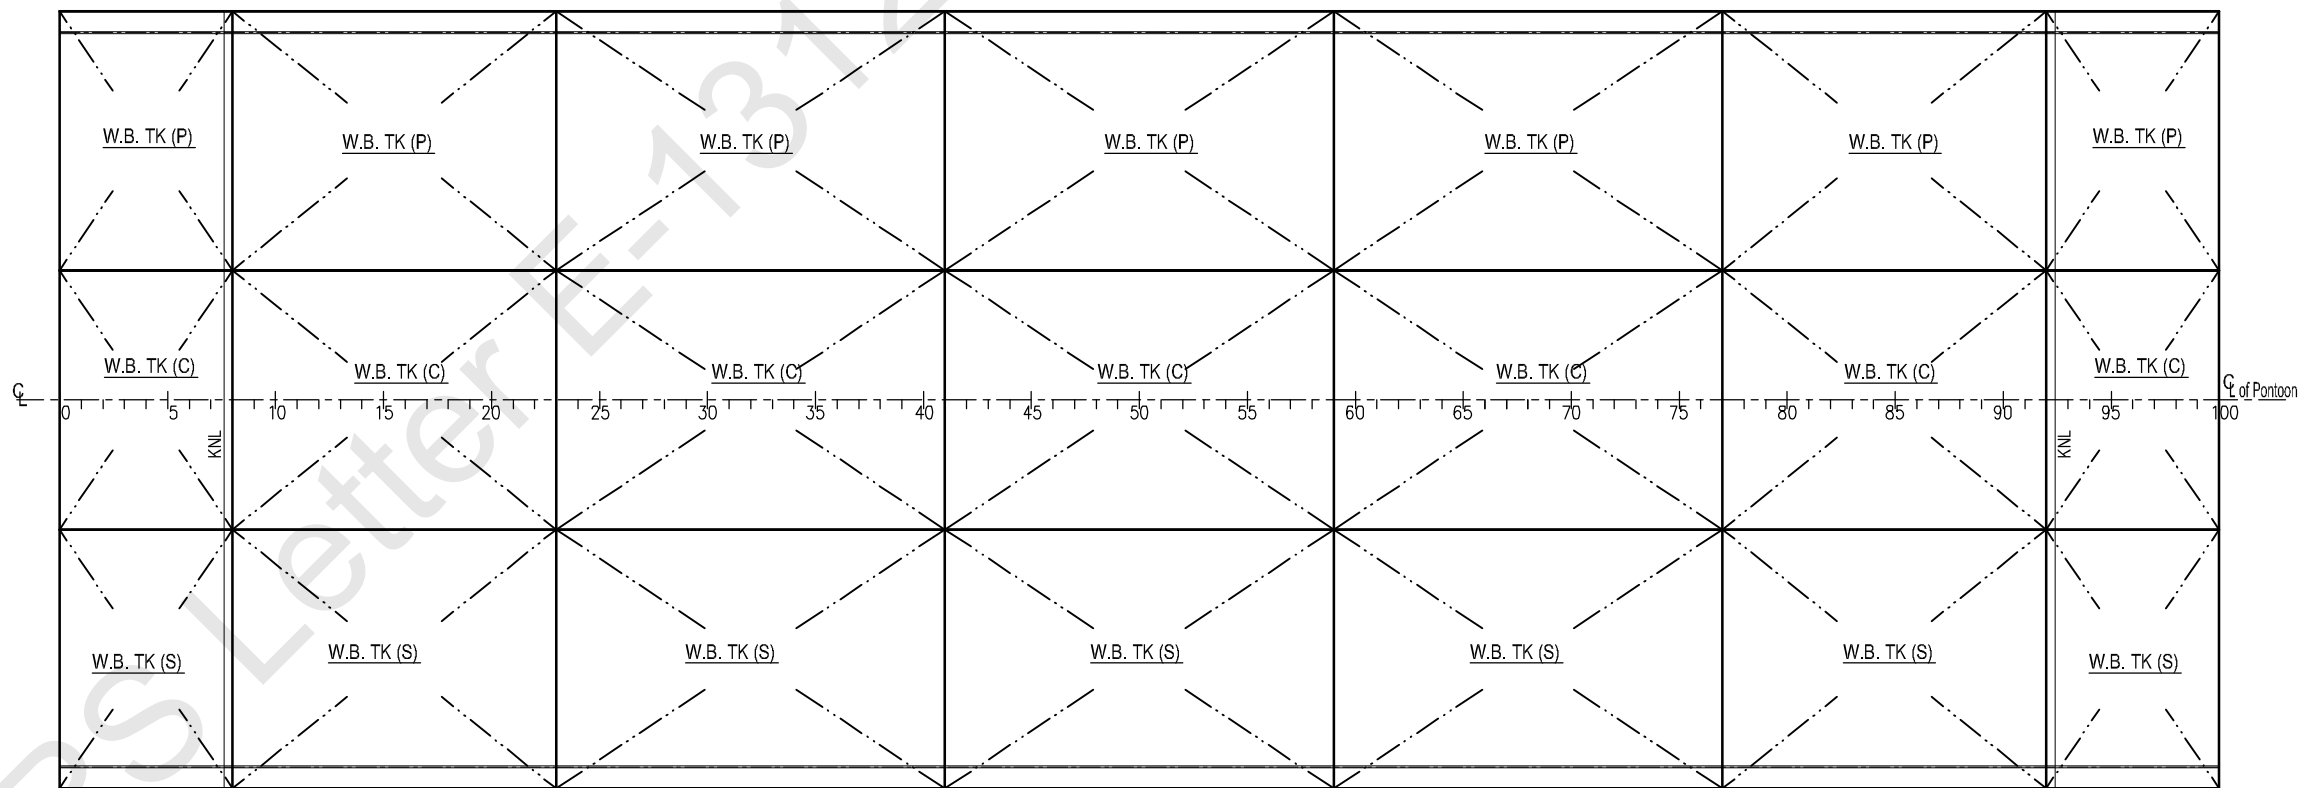

BELOW DECK PLAN

PRINCIPAL PARTICULARS:-

LENGTH O.A	:	50.00 M
BREADTH MLD.	:	18.00 M
DEPTH MLD.	:	3.00 M
DESIGN DRAFT	:	2.20 M
SCANTLING DRAFT	:	2.60 M
FRAME SPG.	:	500 mm

1) CRANE SPECIFICATION:-

CRANE WEIGHT	=	350T
CRANE CAPACITY	=	40 T
WORKING RADIUS	=	35 M

2) CRANE SPECIFICATION:-

CRANE WEIGHT	=	400T
CRANE CAPACITY	=	40 T
WORKING RADIUS	=	30 M

CLASS NOTATION:-

☞ SU, PONTOON, "INDIAN COASTAL SERVICE"

Descriptive Notation: "DECK STRENGTHENED FOR 10 T/M²",
DESCRIPTION "FOR CRANE OPERATION"

NOTE:

- 1) ALL DIMENSION ARE IN MM.
- 2) CRANE WILL OPERATE ONLY IN THE HATCHED REGION.

SEE LETTER E-131246-176069



PLAN(S) NOW SENT SUPERSEDE
THE APPROPRIATE PLAN(S)
PREVIOUSLY APPROVED/NOTED
ON 18.MAY 2021

01	DRAWING REVISED.		23.06.2021	ROHAN	SHAILESH
Rev.#	Description		Date	Drawn	Review
<u>Issued for</u>			<u>Approval</u>		
Client		Project	PONTOON (YARD NO. CHISTI 018)		
<u>K.B. SHIPPING & CO.</u>					
Builder					
<u>CHISTI MARINE SERVICES</u>					
Drg.#	Rev.#	<u>GENERAL ARRANGEMENT</u>		Drawn	ISHWAR
CM21-V-102-0001A	01			Checked	JASIM
Scale	Size			Review-1	MOHIT
1:175	A2			Review-2	SUDHEESH
	Date				
	21.04.2021				
	Sheet				
	1 of 1				



10 Bukit Batok Crescent
#12-01 The Spire
Singapore 658 079
Tel : +65 6316 6513

501 Technocity IT Premises
Plot No X-5/3 Mahape
Navi Mumbai 400 710 India
Tel : +91 22 61462400 (10 Lines)