




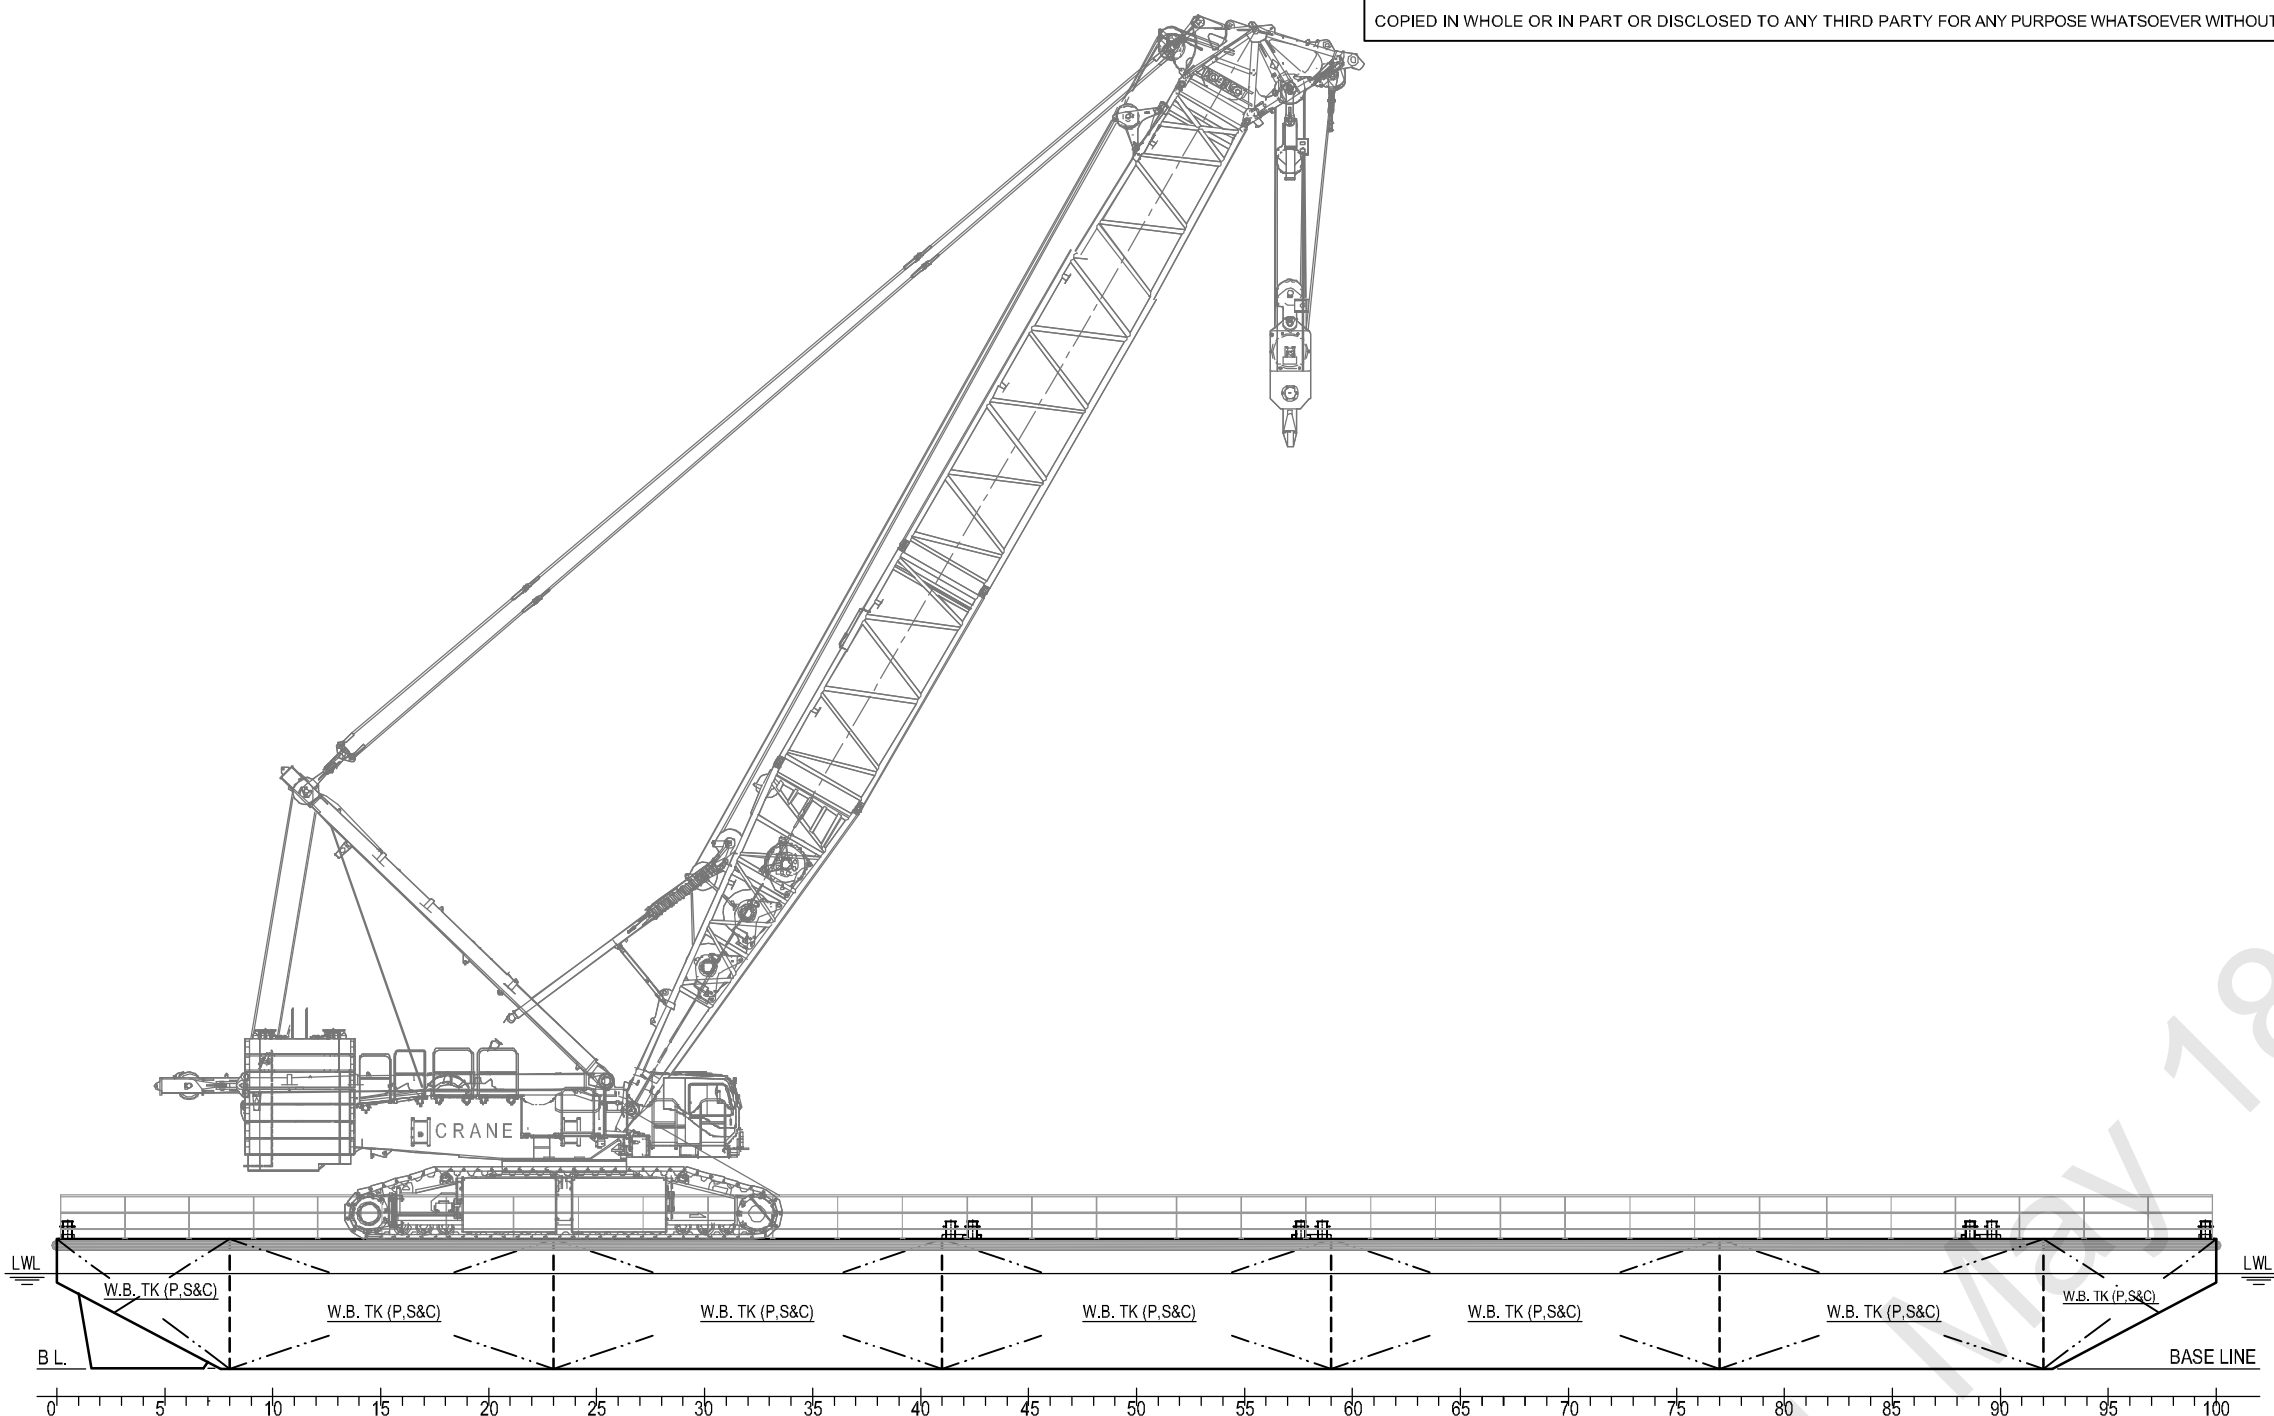

PROFILE

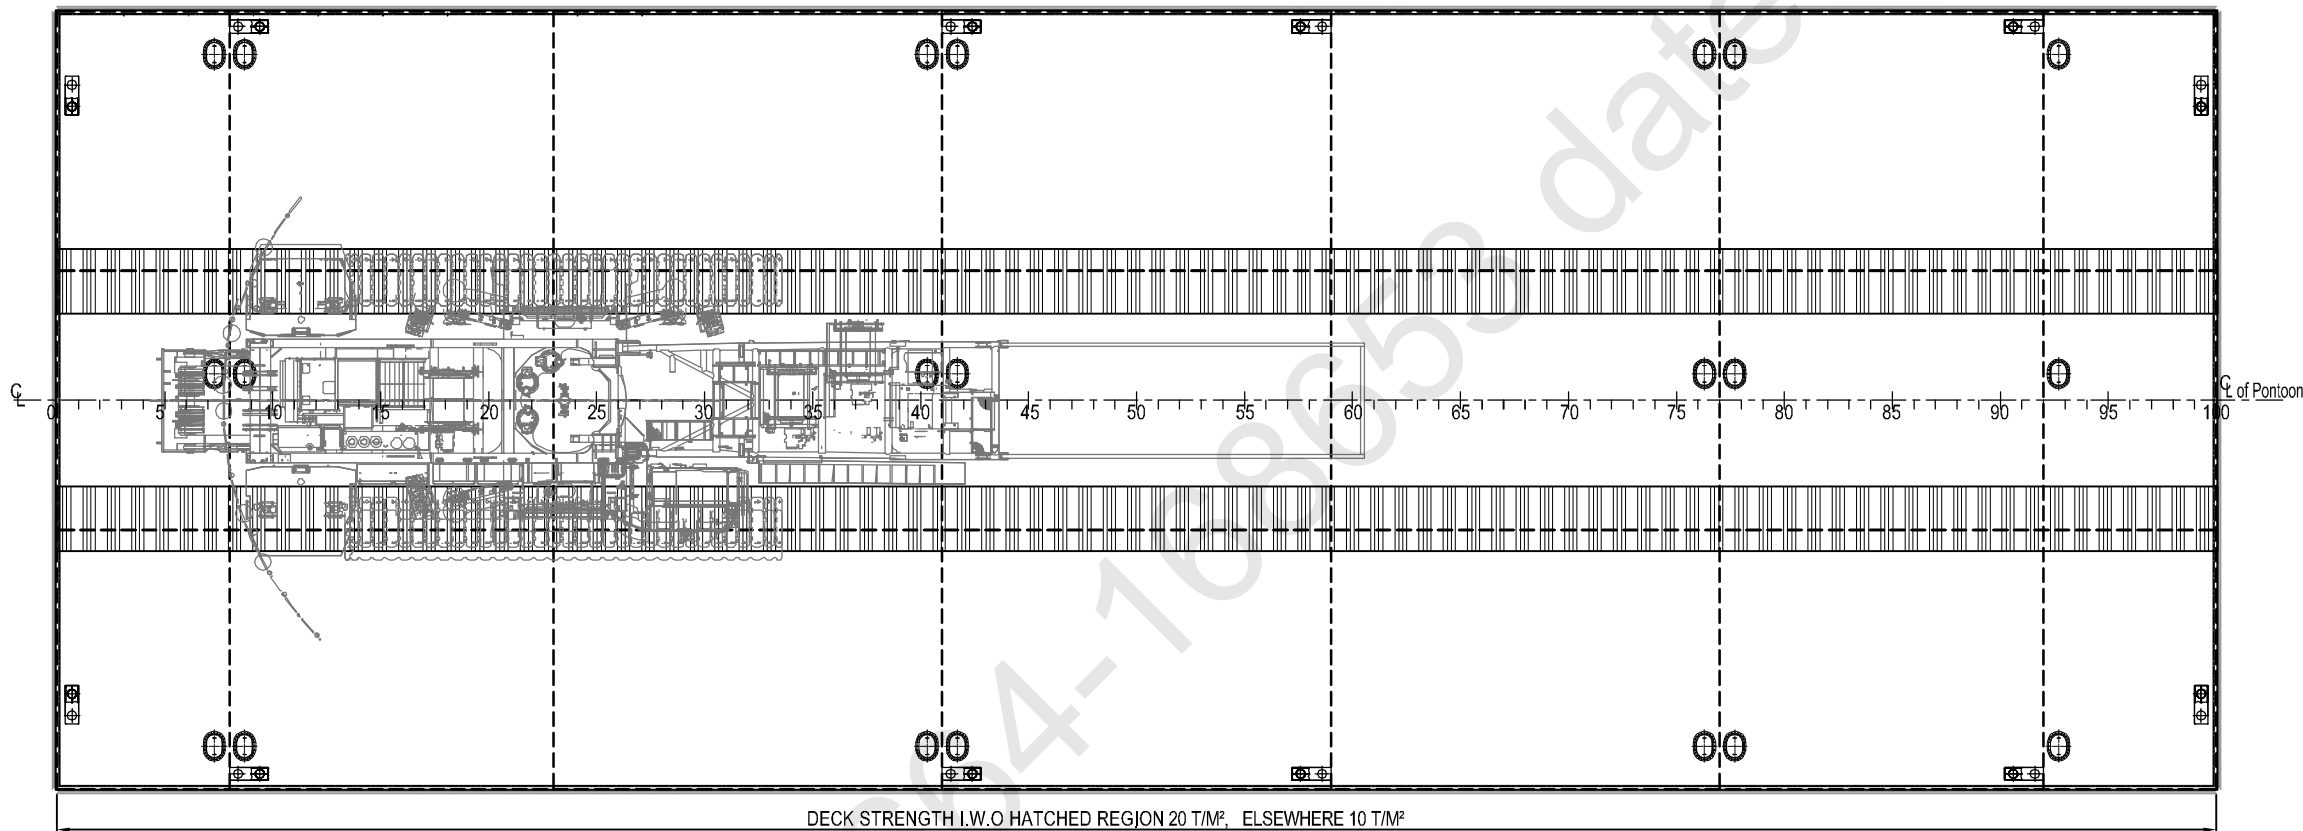

MAIN DECK PLAN

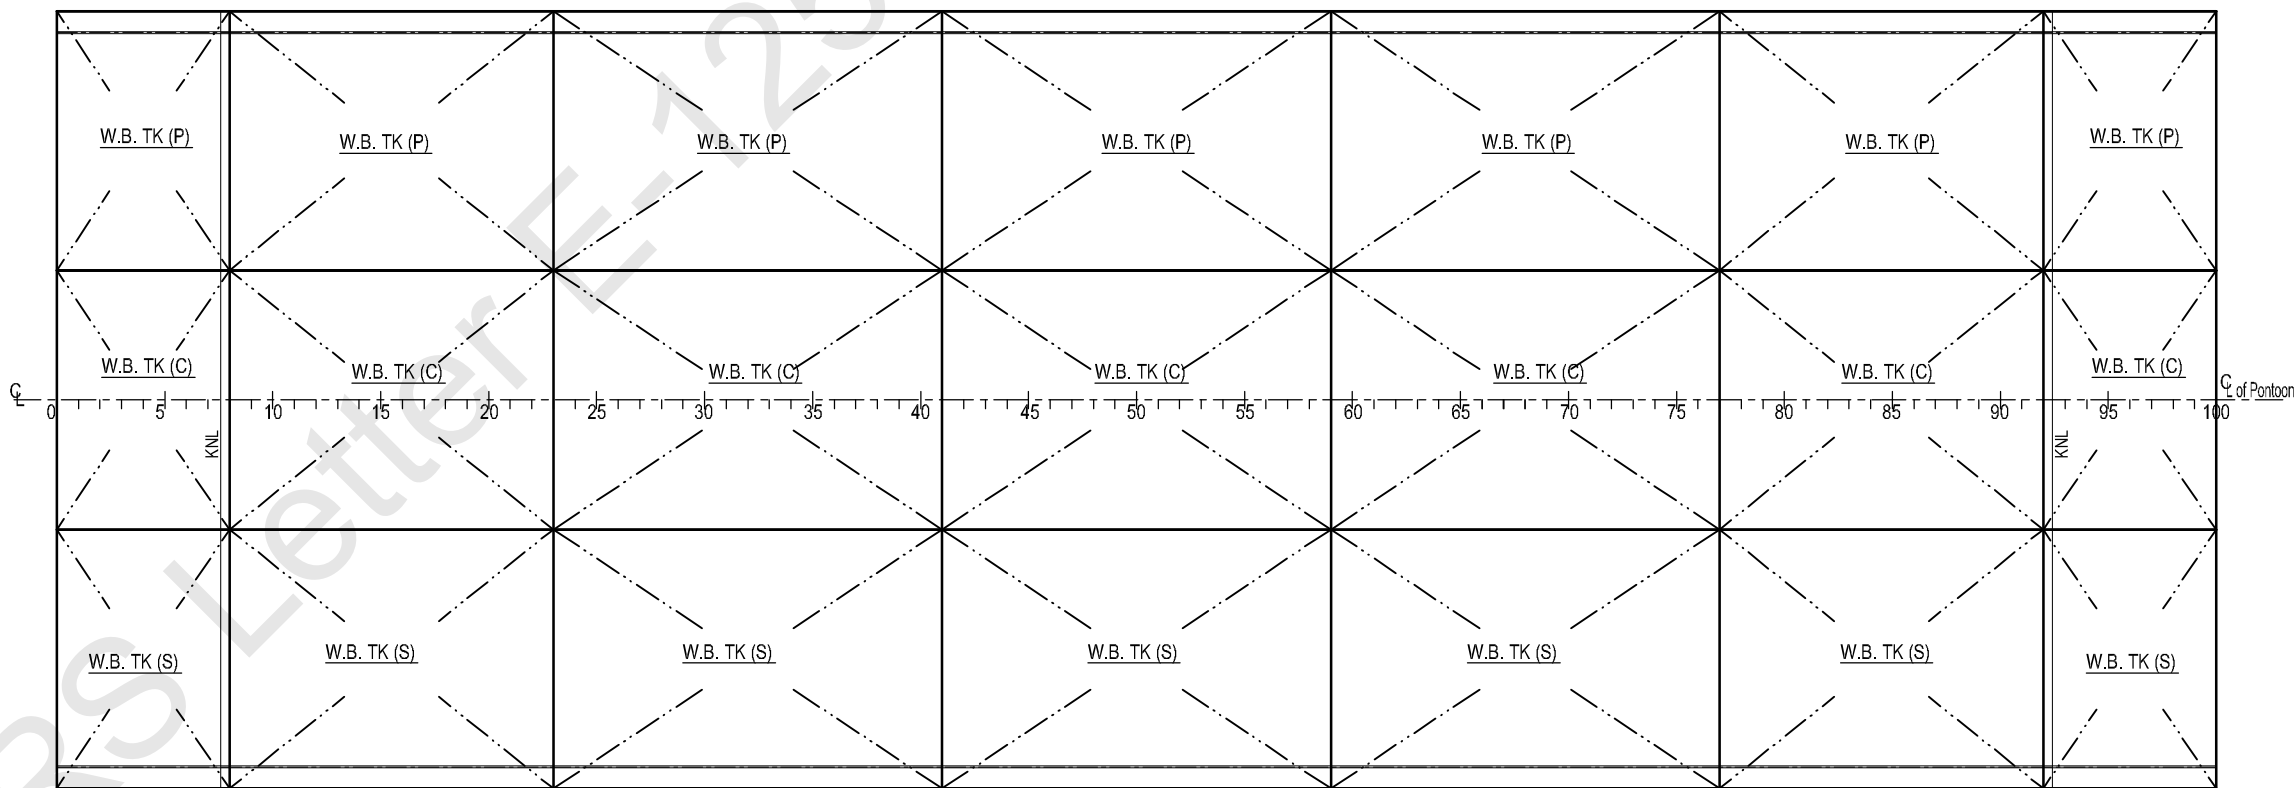

BELOW DECK PLAN

PRINCIPAL PARTICULARS:-

LENGTH O.A.	:	50.00 M
BREADTH MLD.	:	18.00 M
DEPTH MLD.	:	3.00 M
DESIGN DRAFT	:	2.20 M
SCANTLING DRAFT	:	2.60 M
FRAME SPG.	:	500 mm

CRANE SPECIFICATION:-

CRANE WEIGHT	=	350T
CRANE CAPACITY	=	40 T
WORKING RADIUS	=	29 M

SEE LETTER E-125664-168653



CLASS NOTATION:-

SH SU, PONTOON, "INDIAN COASTAL SERVICE"
Descriptive Notation: "DECK STRENGTHENED FOR 10 T/M²",
DESCRIPTION: "FOR CRANE OPERATION"

NOTE:

- 1) ALL DIMENSION ARE IN MM.
- 2) CRANE WILL OPERATE ONLY IN THE HATCHED REGION.

Rev.#	Description	Date	Drawn	Review
Issued for		Approval		
Client		Project		
K.B. SHIPPING & CO.		PONTOON		
Builder		(YARD NO. CHISTI 018 & 019)		
CHISTI MARINE SERVICES				
Drg.#	Rev.#	Drawing Title		Drawn
CM21-V-102-0001	00	GENERAL ARRANGEMENT		ISHWAR
Scale	Size	Date	Sheet	Checked
1:175	A2	21.04.2021	1 of 1	JASIM
				Review-1
				MOHIT
				Review-2
				SUDHEESH



10 Bukit Batok Crescent
#12-01 The Spire
Singapore 658 079
Tel : +65 6316 6513

501 Technocity IT Premises
Plot No X-5/3 Mahape
Navi Mumbai 400 710 India
Tel : +91 22 61462400 (10 Lines)