


BRIDGE DECK

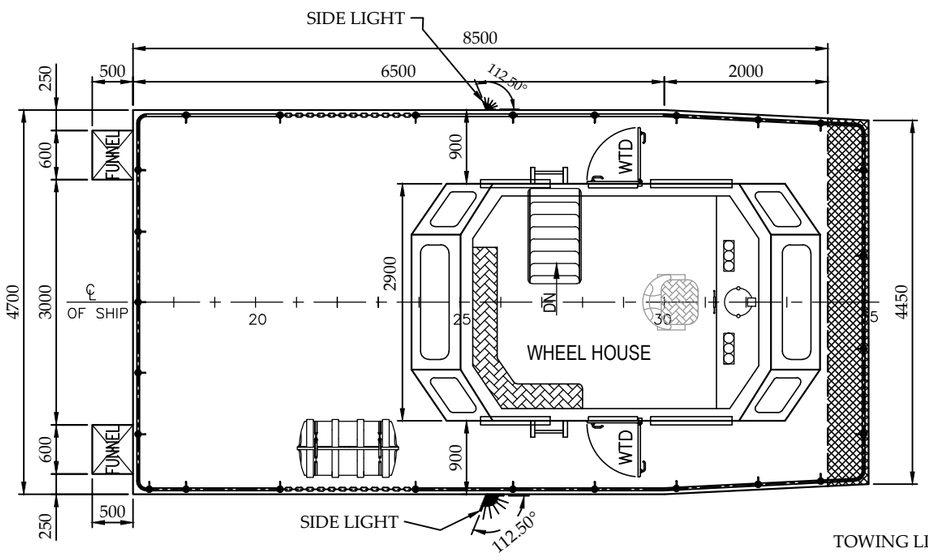


PROFILE




MAIN DECK

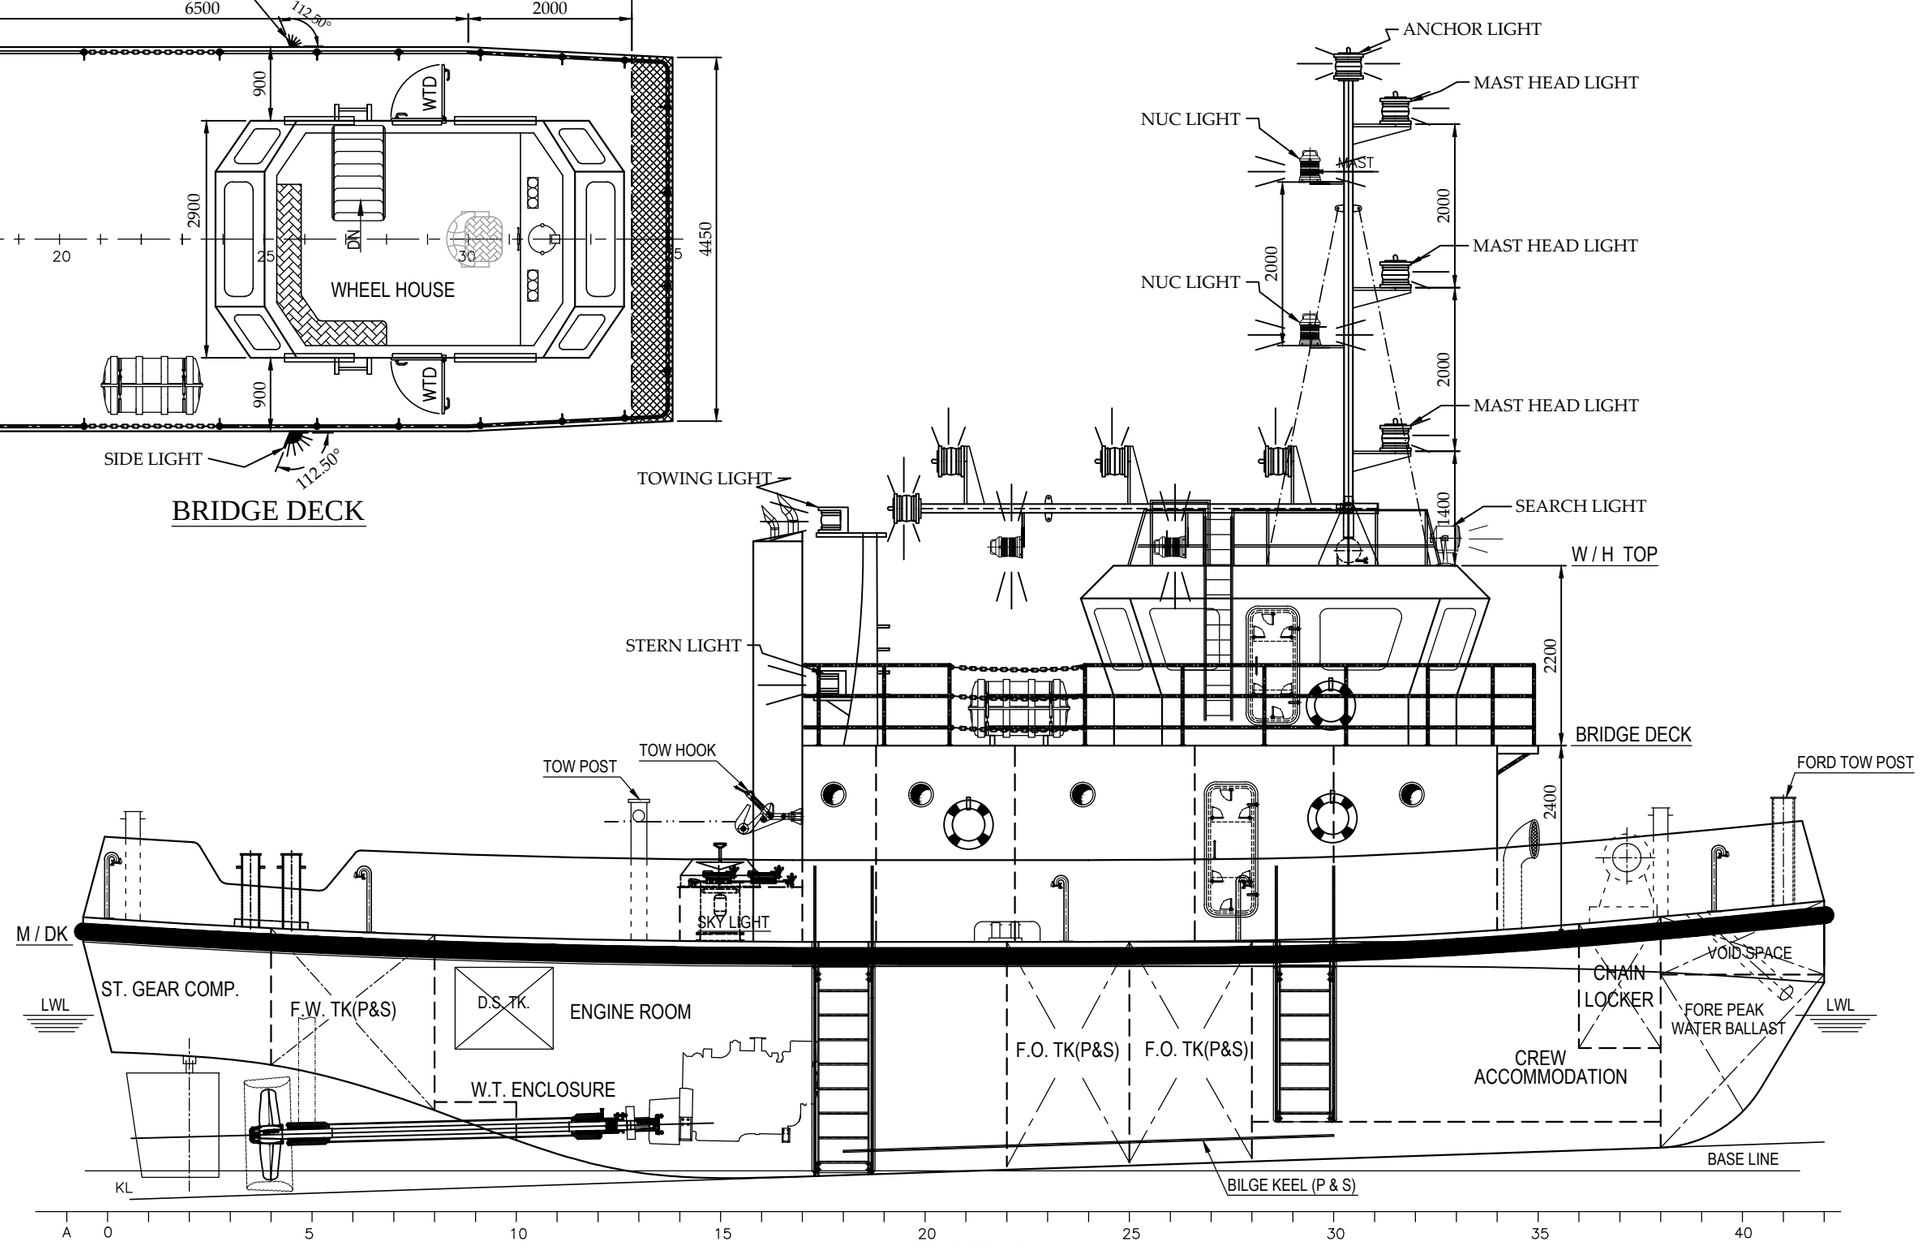


BOTTOM PLAN

INDIAN REGISTER OF SHIPPING
MUMBAI
DATE: 18 Aug 2016
NOTED FOR INFORMATION

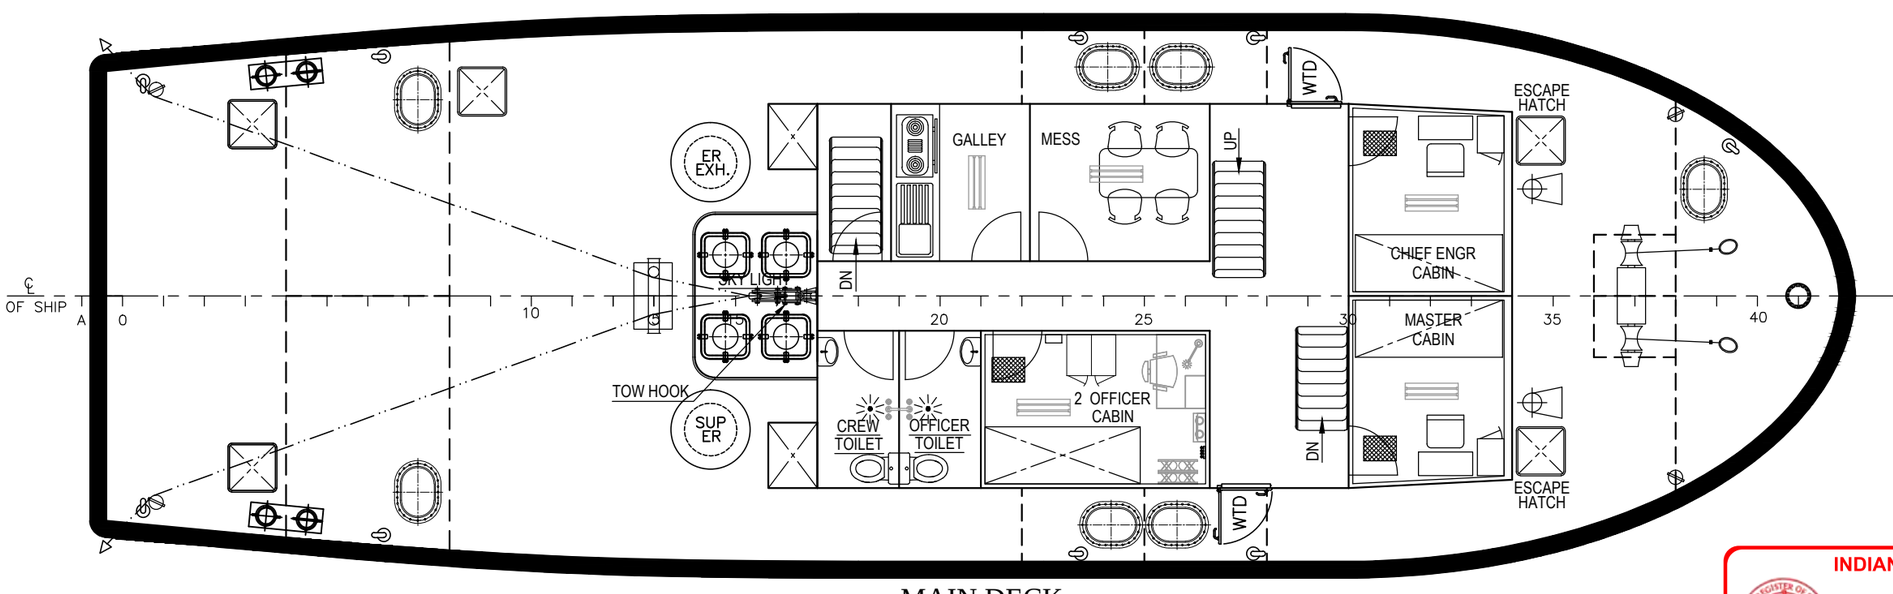SEE LETTER E-39018-47530

SEE LETTER COMMENT NO. 7
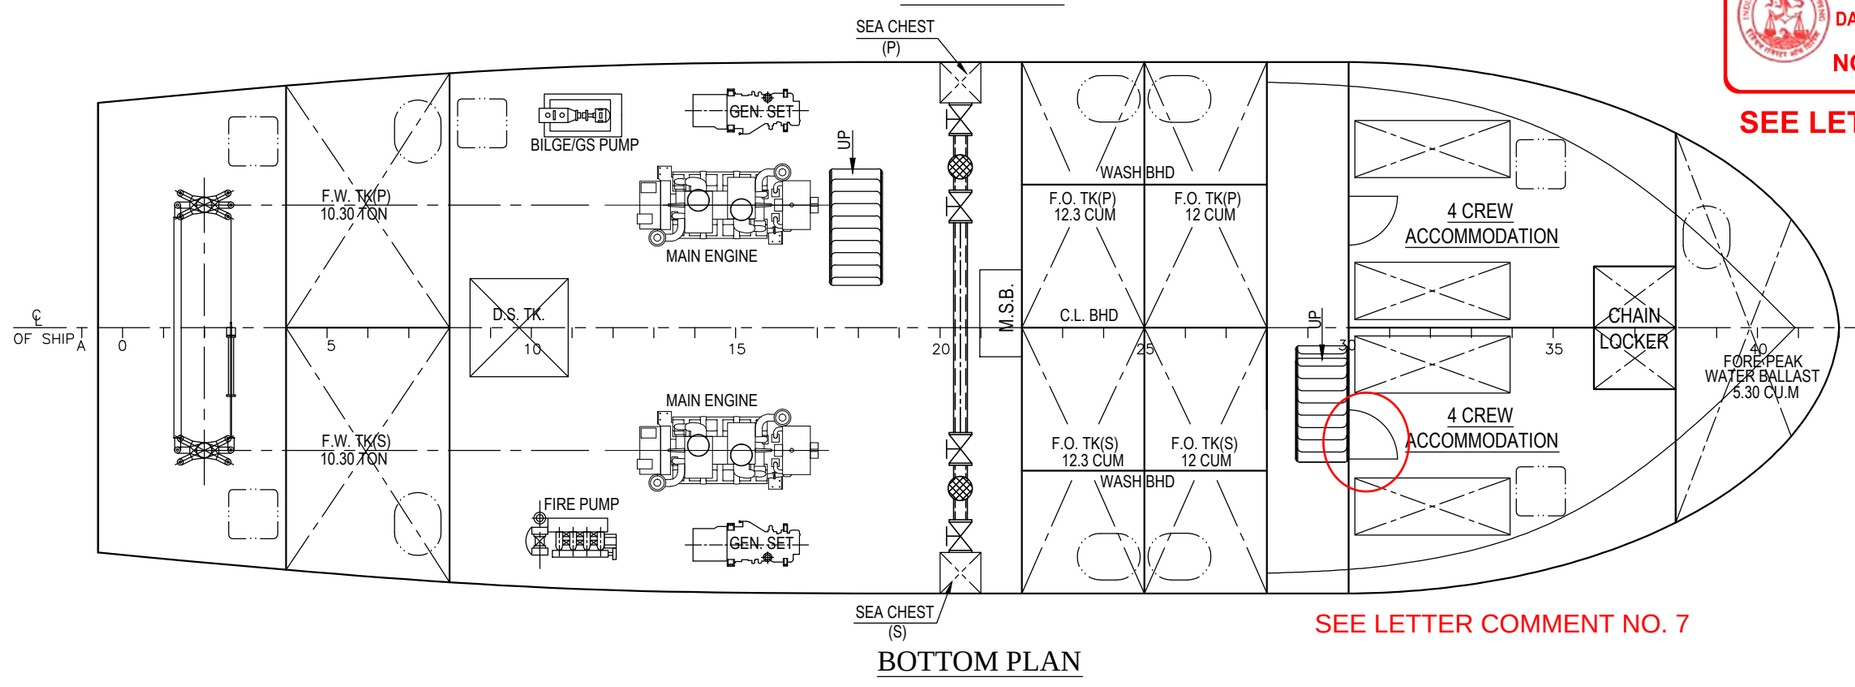
## PRINCIPAL PARTICULARS

| | | |
|---|---|---|
| LENGTH OVERALL | :- | 21.30M |
| LENGTH B.P. | :- | 19.76 M |
| BREADTH | :- | 06.50 M |
| DEPTH | :- | 02.80 M |
| DRAFT(DESIGN) | :- | 01.90 M |
| DRAFT(SCANTLING ) | :- | 02.00M |
| FRAME SPG. | :- | 500 MM |
| BOLLARD PULL | :- | 10 T |
| ENGINE POWER | :- | 2 x 400 BHP |
| DESIGN SPEED | :- | 10 KNOTS |
| COMPLEMENT | :- | 12 PERSONS |
| CLASS NOTATION | :- | [卐] SUL TUG [卐] I Y INDIAN RIVER-SEA VESSEL TYPE - IV |
| CLASS | :- | INDIAN REGISTER OF SHIPPING |
| FUEL OIL | :- | 48.60 CU. MTR |
| FRESH WATER | :- | 20.60 T |

| Rev. | Date | Description | Drawn | Review |
|---|---|---|---|---|
| | | | | |
| | | | | |

Issued for : Client Approval

Client: KB SHIPPING & CO.

Project: 21.30 M TUG BOAT

Drawing Title: GENERAL ARRANGEMENT PLAN

| Drawn | Checked | Review | Date | Scale | Paper | Drawing No :- | Sheet |
|---|---|---|---|---|---|---|---|
| HARSHAD | VG | SC | 20.07.16 | 1:75 | A2 | SBM-16-1011-001 | 1 Of 1 |

S.B. MARINE CONSULTANT
Tel :- 91 22 40244296 , Fax :- 25862318
E-mail : info@sb-marine.com
Web : www.sbmarineconsultant.com

SHIPYARD : CHISTI MARINE ENGINEERING WORKS, SIKKA

YARD NO : 002

THIS DRAWING IS THE PROPERTY OF M/S S.B. MARINE. INFORMATION ARE NOT TO BE TRACED, COPIED OR PUBLISHED BY ANY MANNER, WITHOUT WRITTEN PERMISSION