


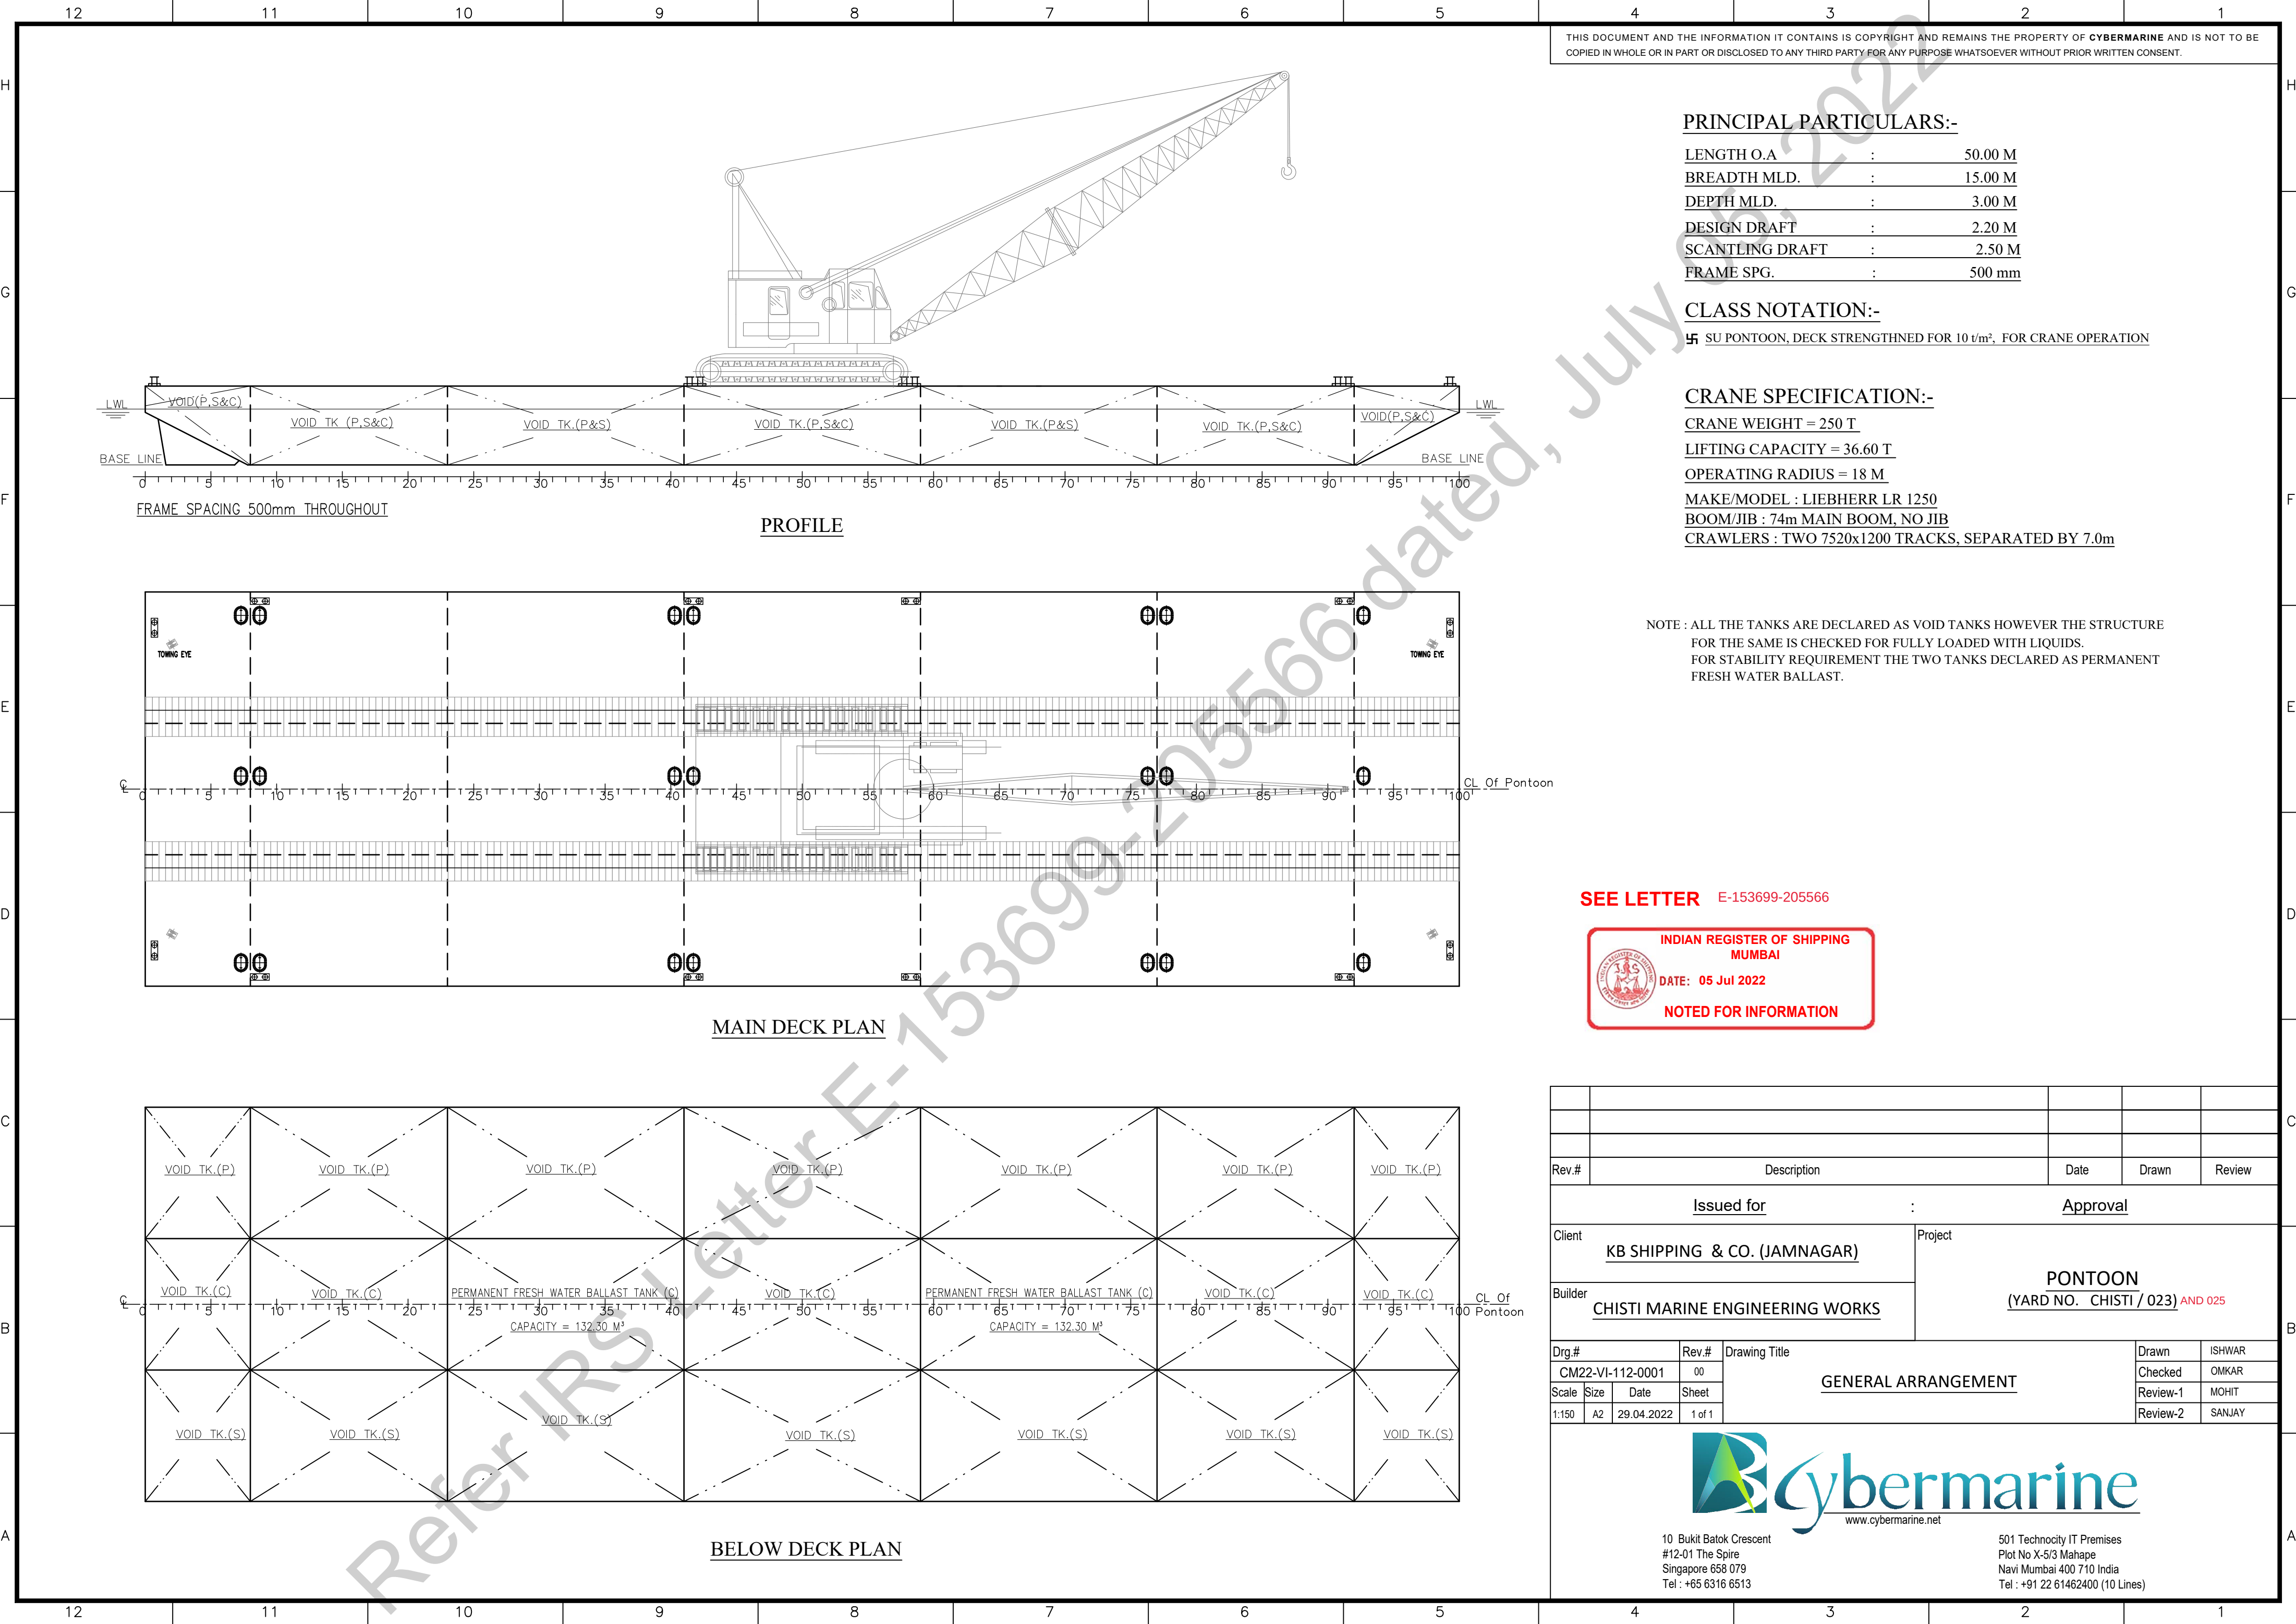

THIS DOCUMENT AND THE INFORMATION IT CONTAINS IS COPYRIGHT AND REMAINS THE PROPERTY OF CYBERMARINE AND IS NOT TO BE COPIED IN WHOLE OR IN PART OR DISCLOSED TO ANY THIRD PARTY FOR ANY PURPOSE WHATSOEVER WITHOUT PRIOR WRITTEN CONSENT.

PRINCIPAL PARTICULARS:-

LENGTH O.A	:	50.00 M
BREADTH MLD.	:	15.00 M
DEPTH MLD.	:	3.00 M
DESIGN DRAFT	:	2.20 M
SCANTLING DRAFT	:	2.50 M
FRAME SPG.	:	500 mm

CLASS NOTATION:-

SU PONTOON, DECK STRENGTHNED FOR 10 t/m², FOR CRANE OPERATION

CRANE SPECIFICATION:-

CRANE WEIGHT = 250 T
LIFTING CAPACITY = 36.60 T
OPERATING RADIUS = 18 M
MAKE/MODEL : LIEBHERR LR 1250
BOOM/JIB : 74m MAIN BOOM, NO JIB
CRAWLERS : TWO 7520x1200 TRACKS, SEPARATED BY 7.0m

NOTE : ALL THE TANKS ARE DECLARED AS VOID TANKS HOWEVER THE STRUCTURE FOR THE SAME IS CHECKED FOR FULLY LOADED WITH LIQUIDS.
FOR STABILITY REQUIREMENT THE TWO TANKS DECLARED AS PERMANENT FRESH WATER BALLAST.

SEE LETTER E-153699-205566



Rev.#	Description		Date	Drawn	Review		
Issued for			Approval				
Client KB SHIPPING & CO. (JAMNAGAR)			Project PONTOON (YARD NO. CHISTI / 023) AND 025				
Builder CHISTI MARINE ENGINEERING WORKS							
Drg.#		Rev.#	Drawing Title GENERAL ARRANGEMENT		Drawn	ISHWAR	
CM22-VI-112-0001		00			Checked	OMKAR	
Scale	Size	Date			Sheet	Review-1	MOHIT
1:150	A2	29.04.2022			1 of 1	Review-2	SANJAY



10 Bukit Batok Crescent
#12-01 The Spire
Singapore 658 079
Tel : +65 6316 6513

501 Technocity IT Premises
Plot No X-5/3 Mahape
Navi Mumbai 400 710 India
Tel : +91 22 61462400 (10 Lines)