




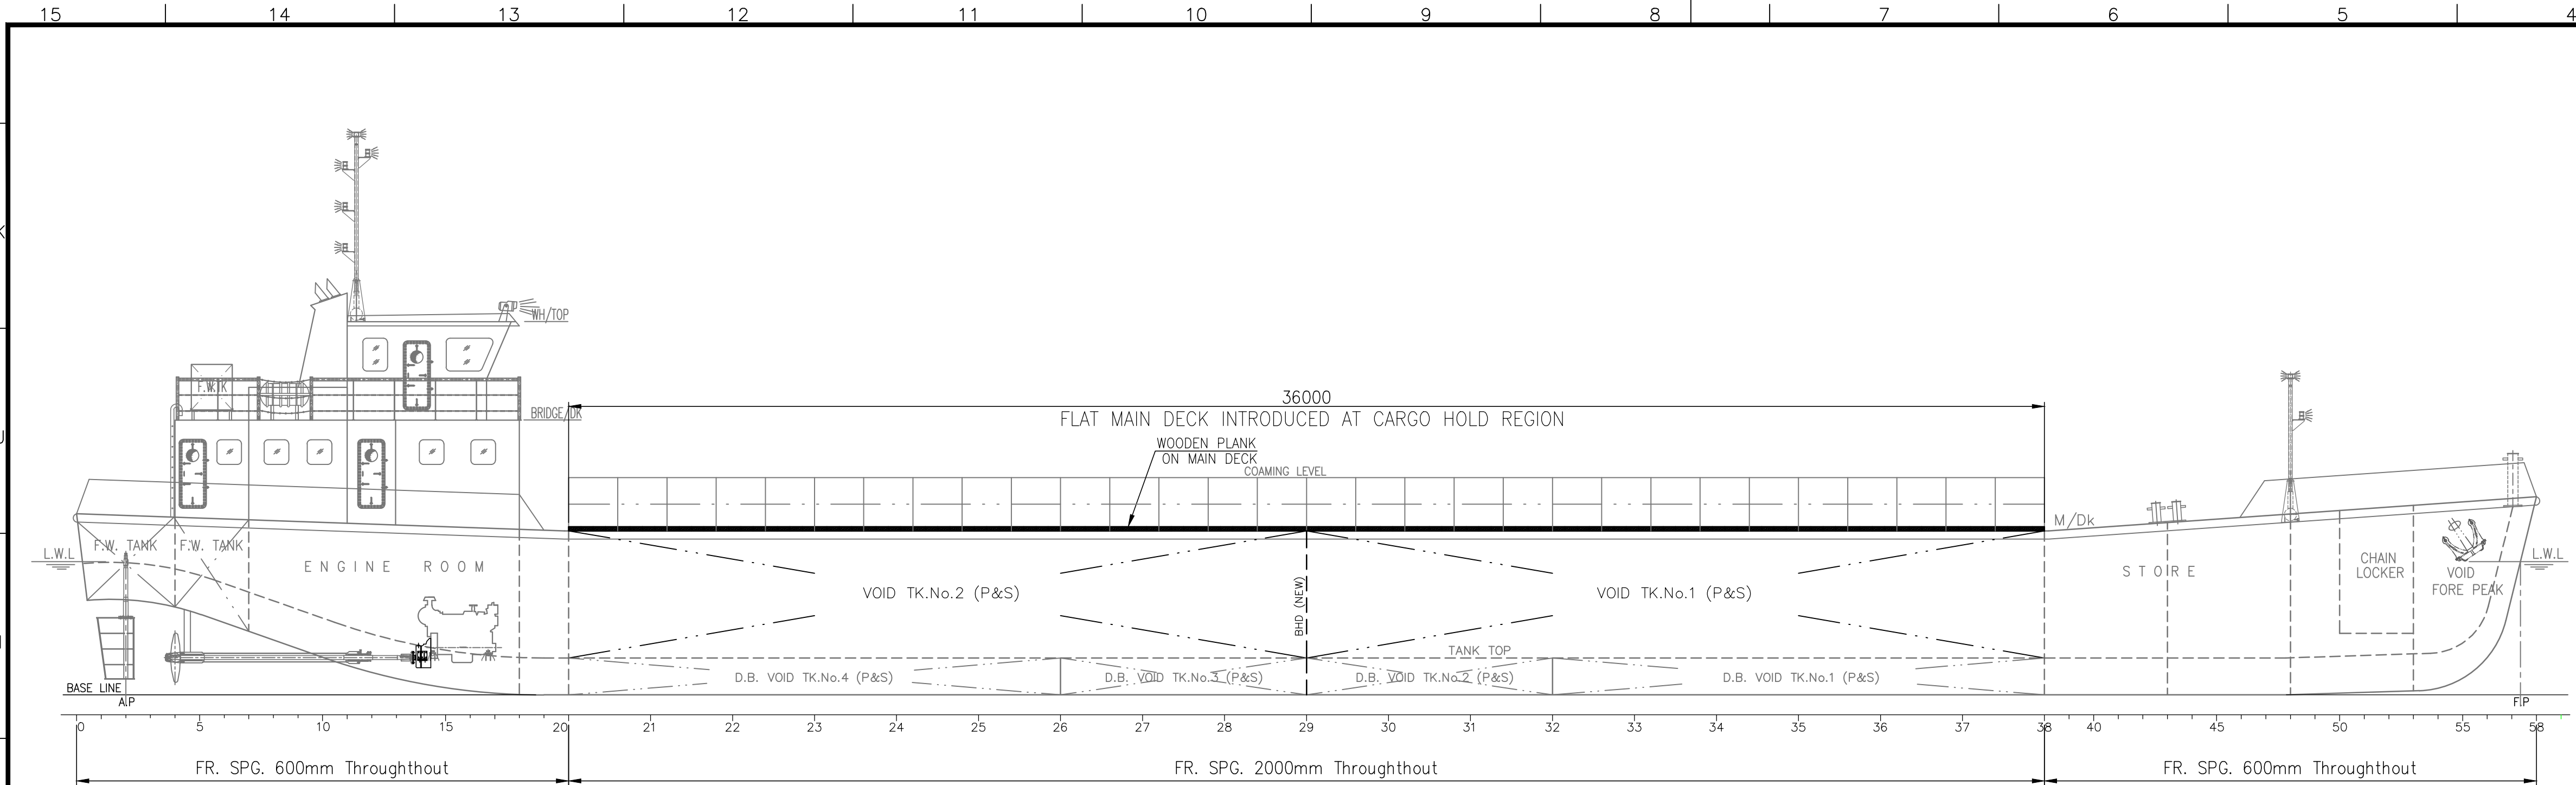

PROFILE

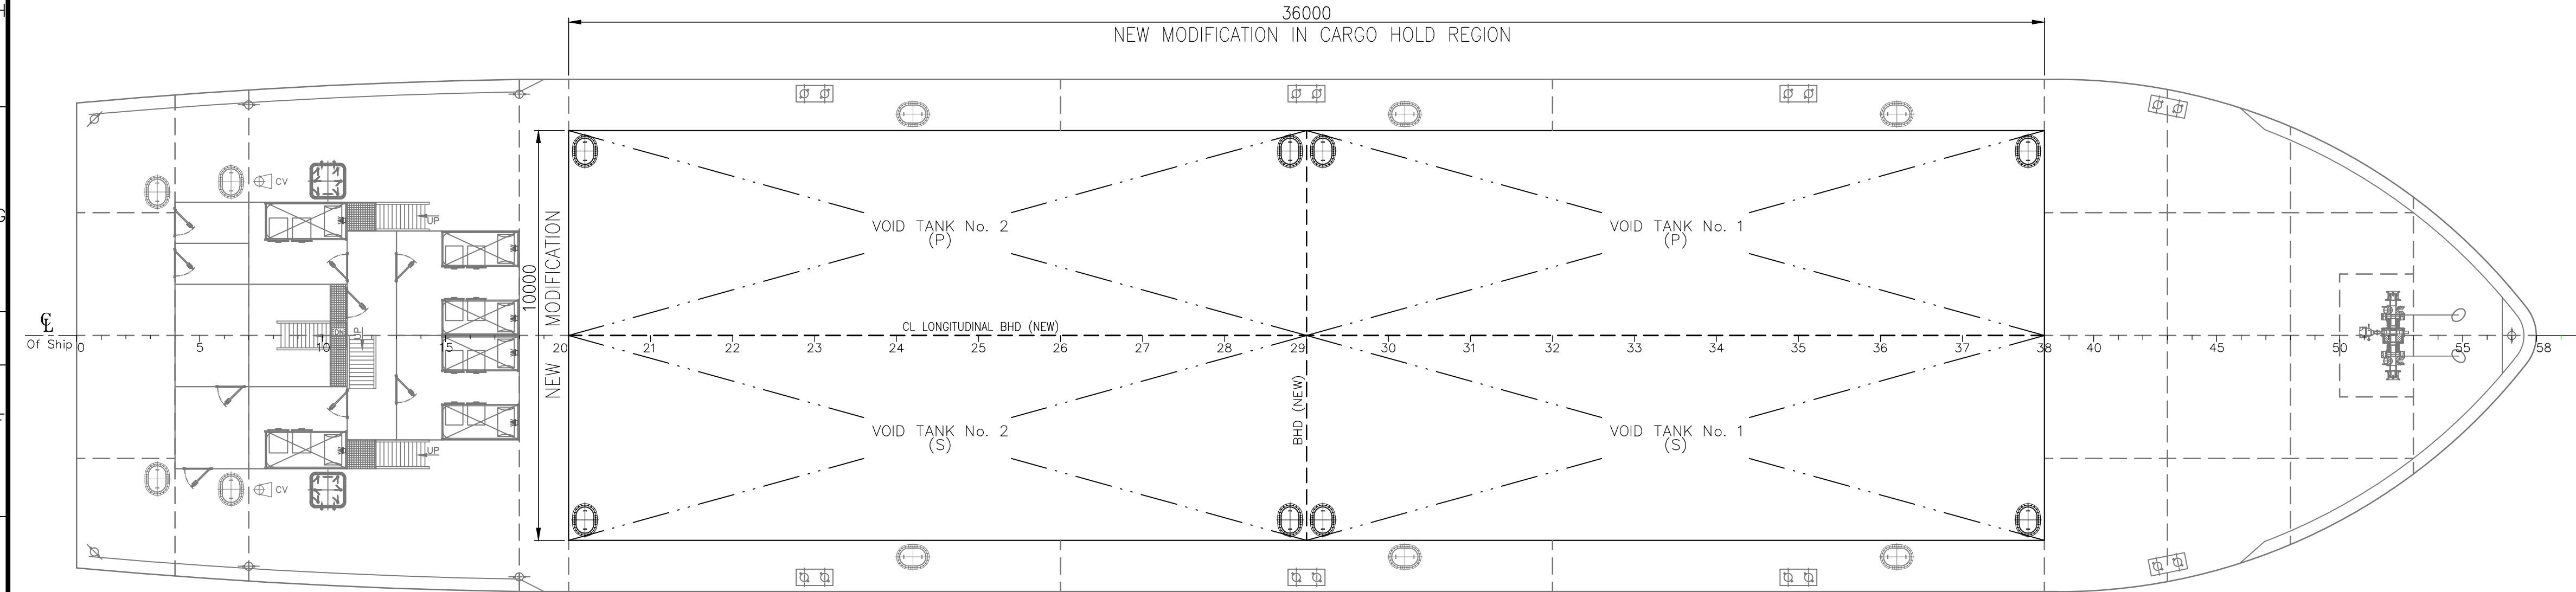

MAIN DECK PLAN

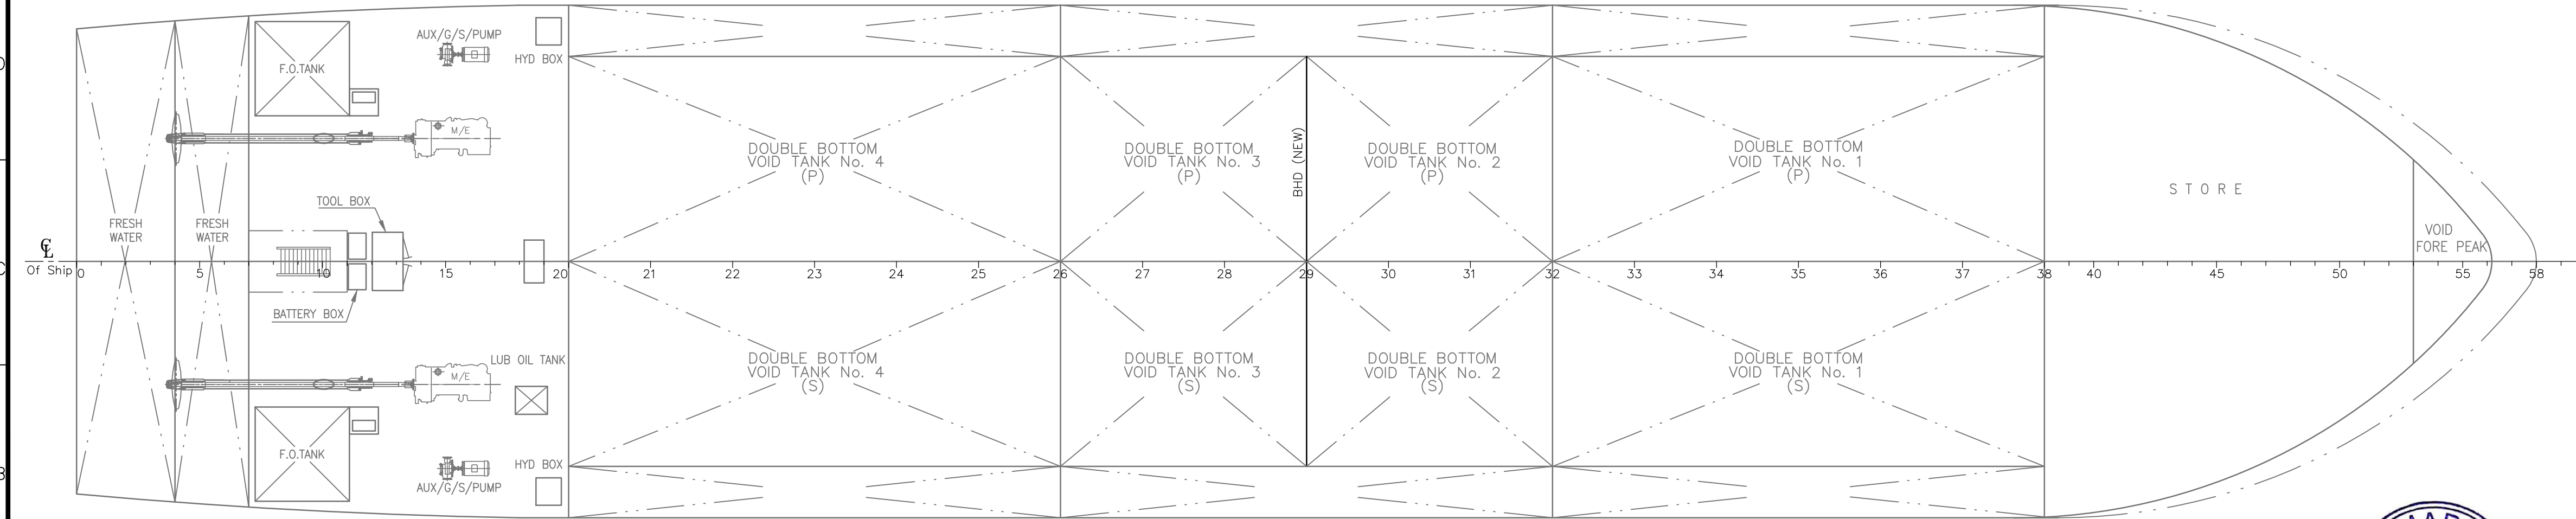

BOTTOM PLAN



MAIN PARTICULARS (CONVERTED)

VESSEL NAME	MV ZARAH-II
TYPE	DECK CARGO BARGE
LENGTH O.A.	60.00M
BREADTH	12.50M
DEPTH	4.00M
DRAFT	2.80M
MAXIMUM DECK CARGO	800 TON
DECK STRENGTH	15 TON . SQM
AREA OF OPERATION	INLAND WATER
SPEED	8 KNOTS


CAPACITIES :

COMPLEMENTS	9 CREW
FUEL OIL STORAGE	13 M.T
FRESH WATER STORAGE	12 M.T

PROPULSION MACHINERIES :

MAIN ENGINE :-	CUMMINS MAKE NT-855M (BC)
	270HP @1800 RPM
GEAR BOX :-	KPC MAKE MG 514
	4.14 : 1 RATIO x 2NOS

ANCHOR WINDLASS :	DIESEL ENGINE DRIVEN
STEERING GEAR :	HAND & SEMI HYDRALIC
G.S. PUMPS :	32M ³ x 2NOS.
GENSET :	15 KVA x 1NO.

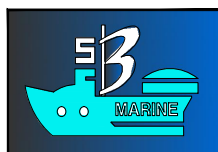Rev.	Date	Description						Drawn	Review
Issued for						:	Client Approval		
Client :-		ARCADIA SHIPPING & TRADING CO.							
Project :-		CONVERSION OF M.V. ZARAH - II TO FLAT TOP DECK LOADING BARGE							
Drawing Title :-		GENERAL ARRANGEMENT PLAN							
Drawn	Checked	Review	Date	Scale	Paper	Rev #	Drawing No :-		Sheet
Kunal	AKP	SC	27.01.21	1:100	A1	00	S B M - 2 0 - 2 0 1 8 - 0 0 1		1 Of 1
 S.B. MARINE CONSULTANT Tel : + 91 22 25970189 E-mail : info@sb-marine.com Web : www.sbmarineconsultant.com							Builder :-		
							Yard No :-		

THIS DRAWING IS THE PROPERTY OF M/S S.B. MARINE. INFORMATION ARE NOT TO BE TRACED, COPIED OR PUBLISHED BY ANY MANNER, WITHOUT WRITTEN PERMISSION